
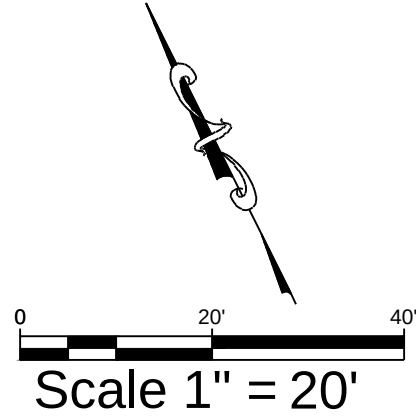


ORIGINAL LAYOUT SIZE: 24x36
©2026 H:\JOBFILES\13\13.13 BUILDING GROUP\13.13 70496 VALLEY VIEW TOWNHOMES SP104 CADPLOT SHEET\UTILITY TAP PLAN.DWG 2/27/2026 10:11 AM Chris Shaleesh

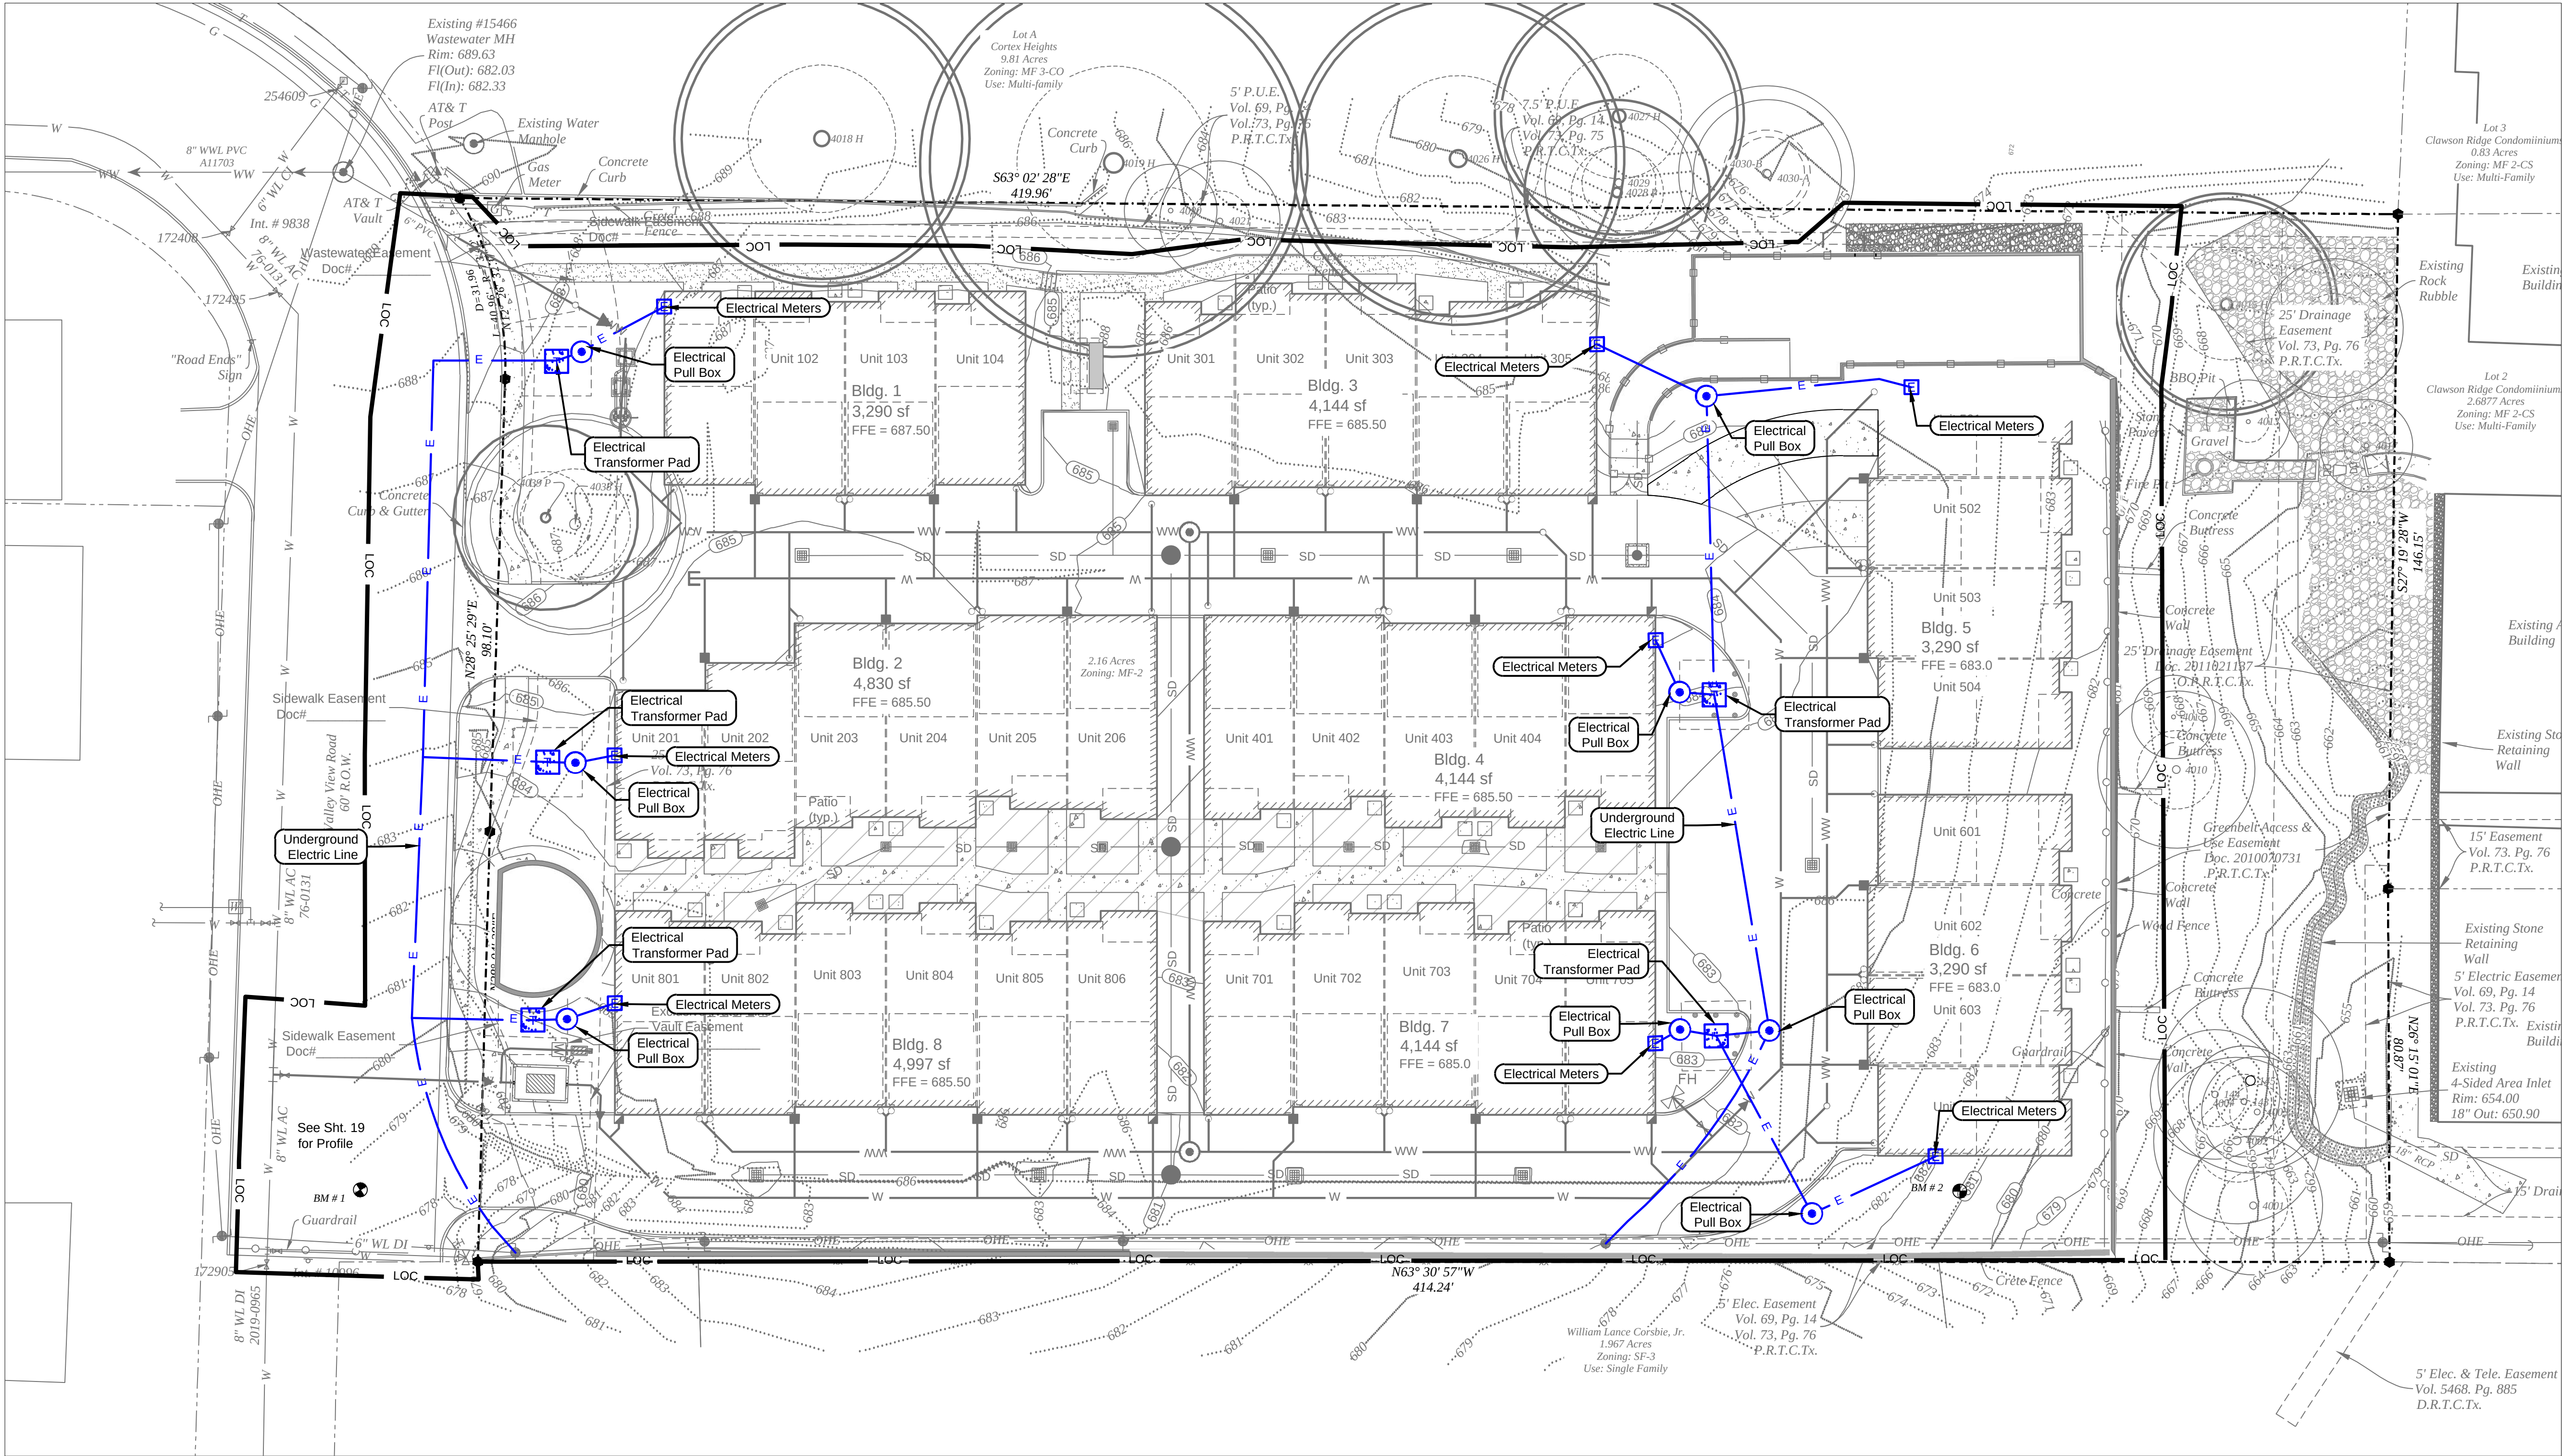

Note

This project is subject to the Void and Water Flow Mitigation Rule (COA ECM 1.12.0 and COA Item No. 658S of the SSM) provision that all trenching greater than 5 feet deep must be inspected by a geologist (Texas P.G.) or a geologist's representative.

Tree List

Refer to landscape plan sheet 32 for the tree list.

Benchmarks

B.M. #1 - Mag Nail Set in Asphalt
Elevation = 678.52' NAVD 88 (GEOID 18)

B.M. #2 - Mag Nail Set in Asphalt
Elevation = 681.08' NAVD 88 (GEOID 18)

Legal Description

Lot 1, Mecey Subdivision Volume 73, Page 76, Plat Records of Travis County, Texas.



Utility Notes

- Contractor shall verify horizontal and vertical location of existing utilities prior to construction.
- Contractor shall verify location of existing line, point of connection and notify engineer of any conflicts/discrepancies prior to installation of improvements.
- All Private Domestic Water Branches to the buildings are to be 2" HDPE service tube per Detail 520-AW-01B
- All Private Wastewater Branches to the building are to be 6" PVC service connections per Detail 520-AW-01C

Release of this application does not constitute a verification of all data, information and calculations supplied by the applicant. The engineer of record is solely responsible for the completeness, accuracy and adequacy of his/her submittal, whether or not the application is reviewed for Code compliance by City engineers.

The location of all existing utilities shown on these plans has been based upon record information only and may not match locations as constructed. The contractor shall contact Texas 811 for assistance in determining existing utility locations prior to beginning construction. Contractor shall field verify locations of utility crossings prior to beginning construction.

Preliminary Electrical Design Plan

Valley View Townhomes

3759 Valley View Road
Austin, Texas 78704
Travis County

Bleyl Engineering

Planning • Design • Management

7701 San Felipe Blvd., Suite 200, Austin TX 78729
Texas Firm Registration No. F-678

Tel: 512-454-2400

www.bleylengineering.com

Austin Bryan Conroe Houston



Design: CS, JR
CAD: JW, CS Review: JKR
Project No: RJ3 70496

Sheet: **21** of **39**
SP-2025-0126C