

PROFESSIONAL SEAL:



DATE SEALED: 02/13/2026

PROJECT NAME:

VALLEY VIEW
TOWNHOMES

OWNER:

WM 41 AUSTIN
RE, LLC

PROJECT LOCATION:

3759 VALLEY
VIEW ROAD,
AUSTIN,
TEXAS 78704


REVISIONS:

PROJECT #: 010-25-01
ORIGINAL ISSUE: 02/13/2026

DRAWING TITLE:
ROOT ZONE
IMPACT EXHIBIT


SHEET NO.:

31 of 35

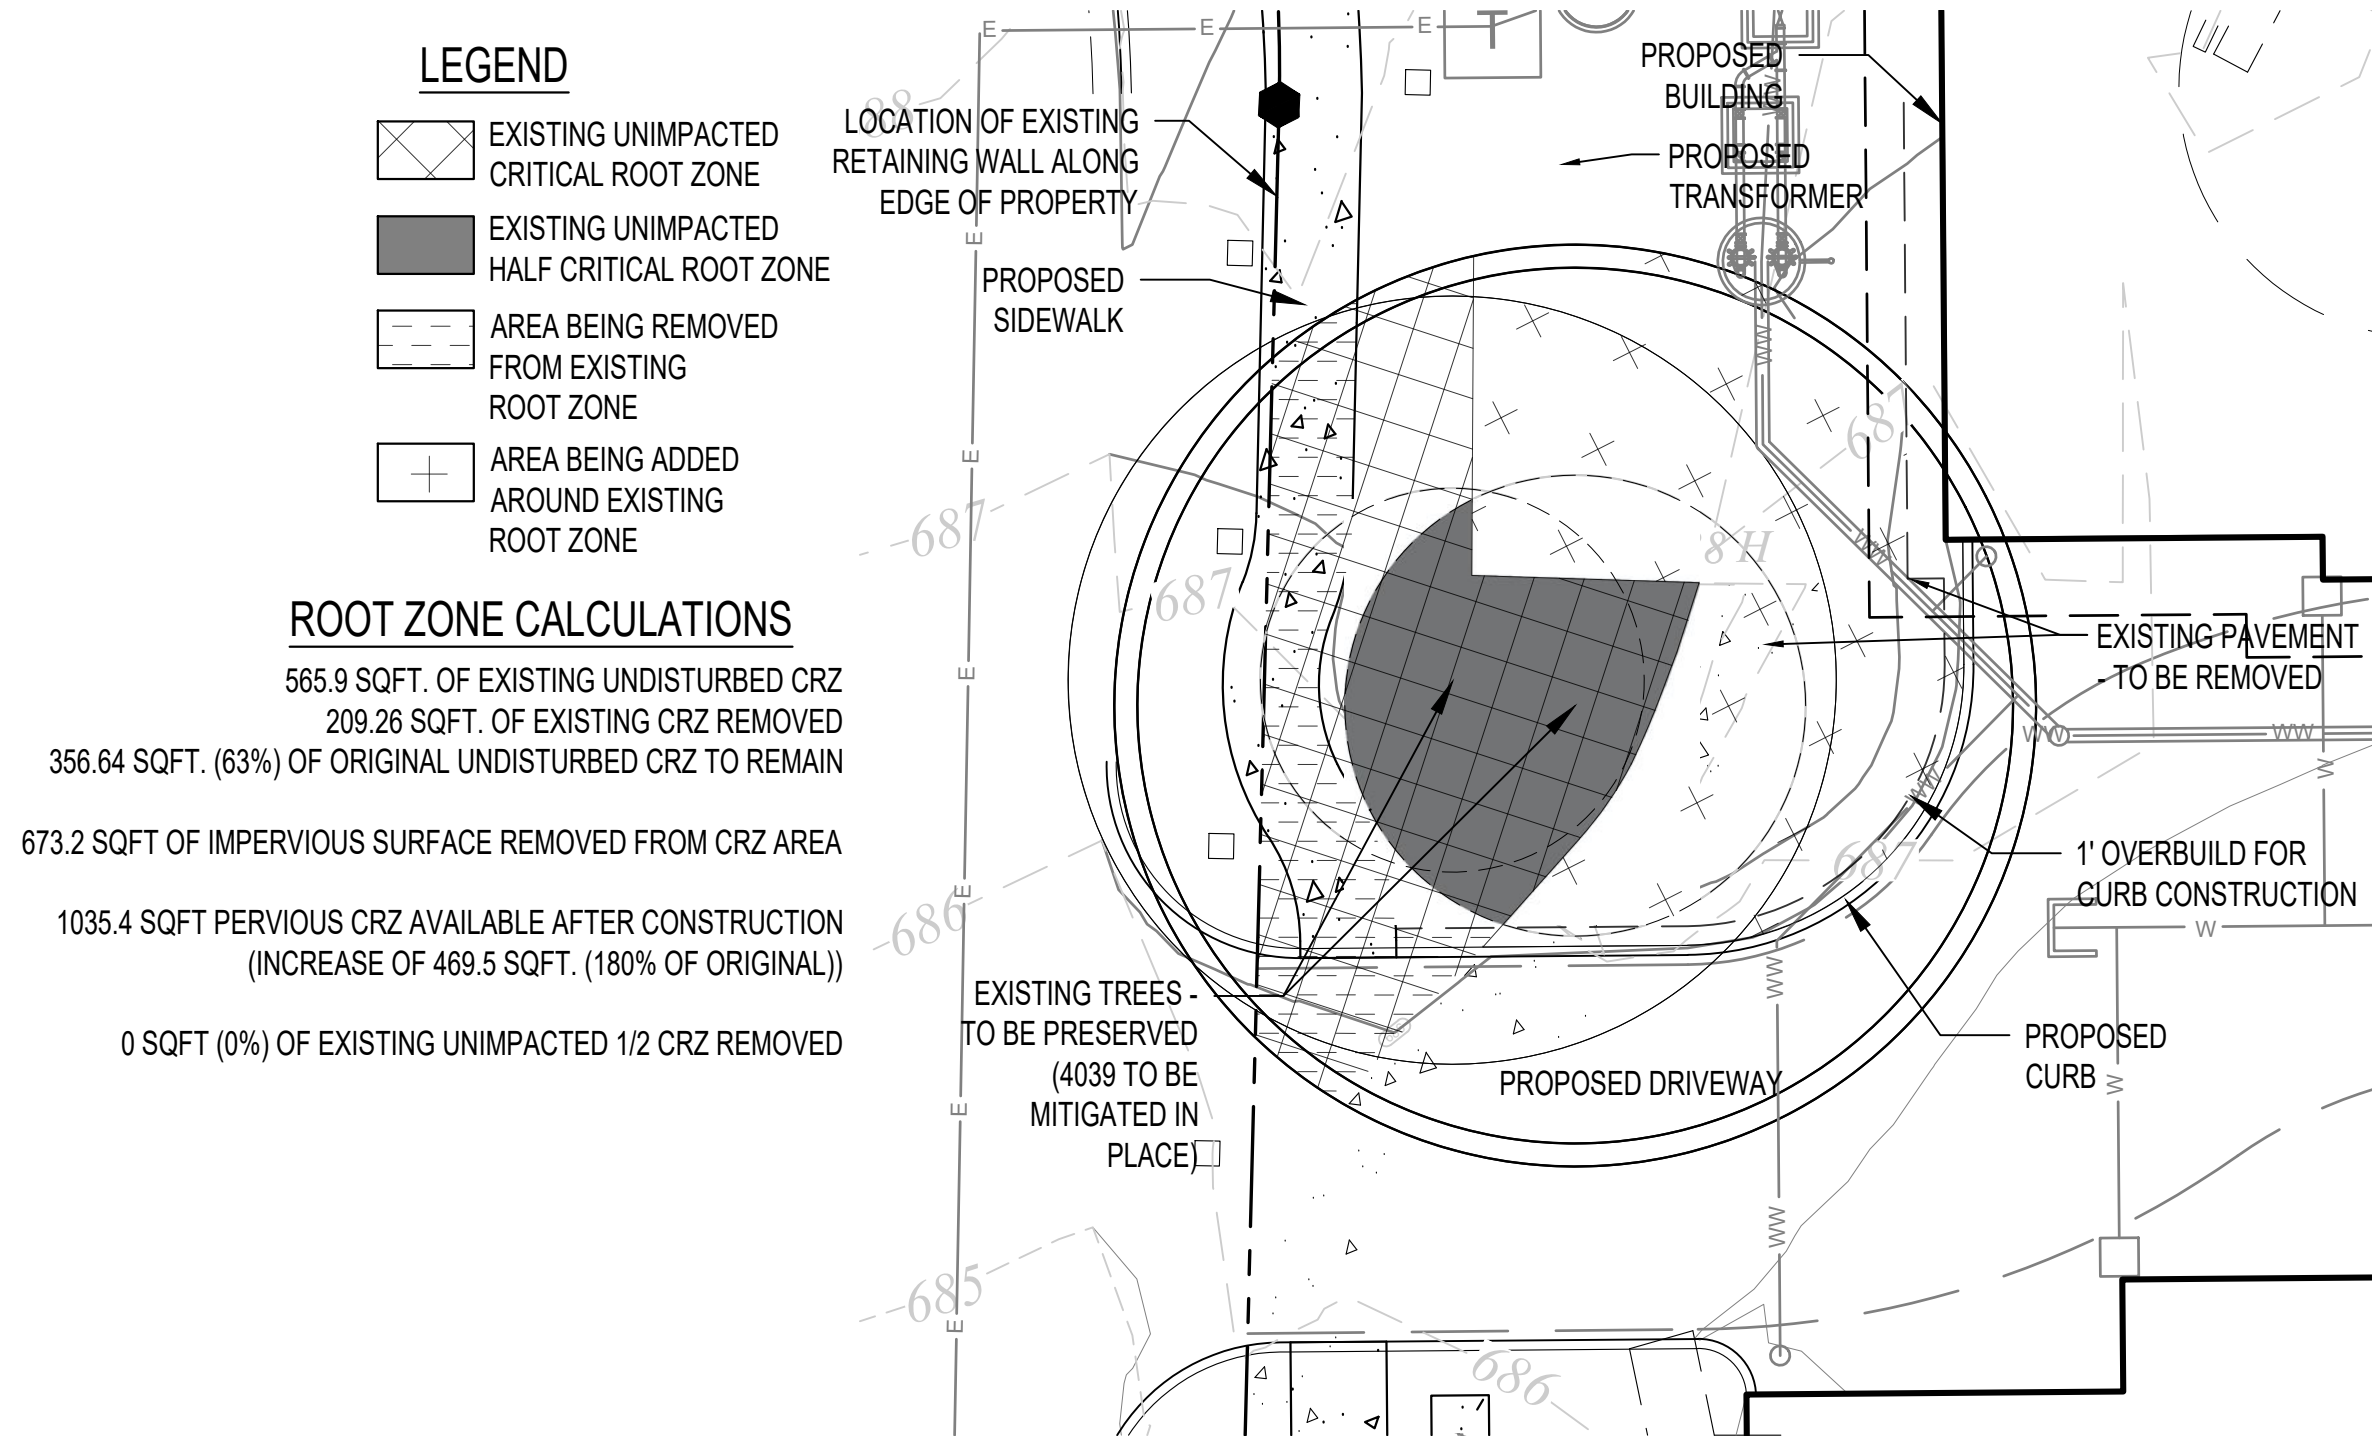

2 CRITICAL ROOT ZONE IMPACT TREE 4038H

Scale: 1" = 10'-0"

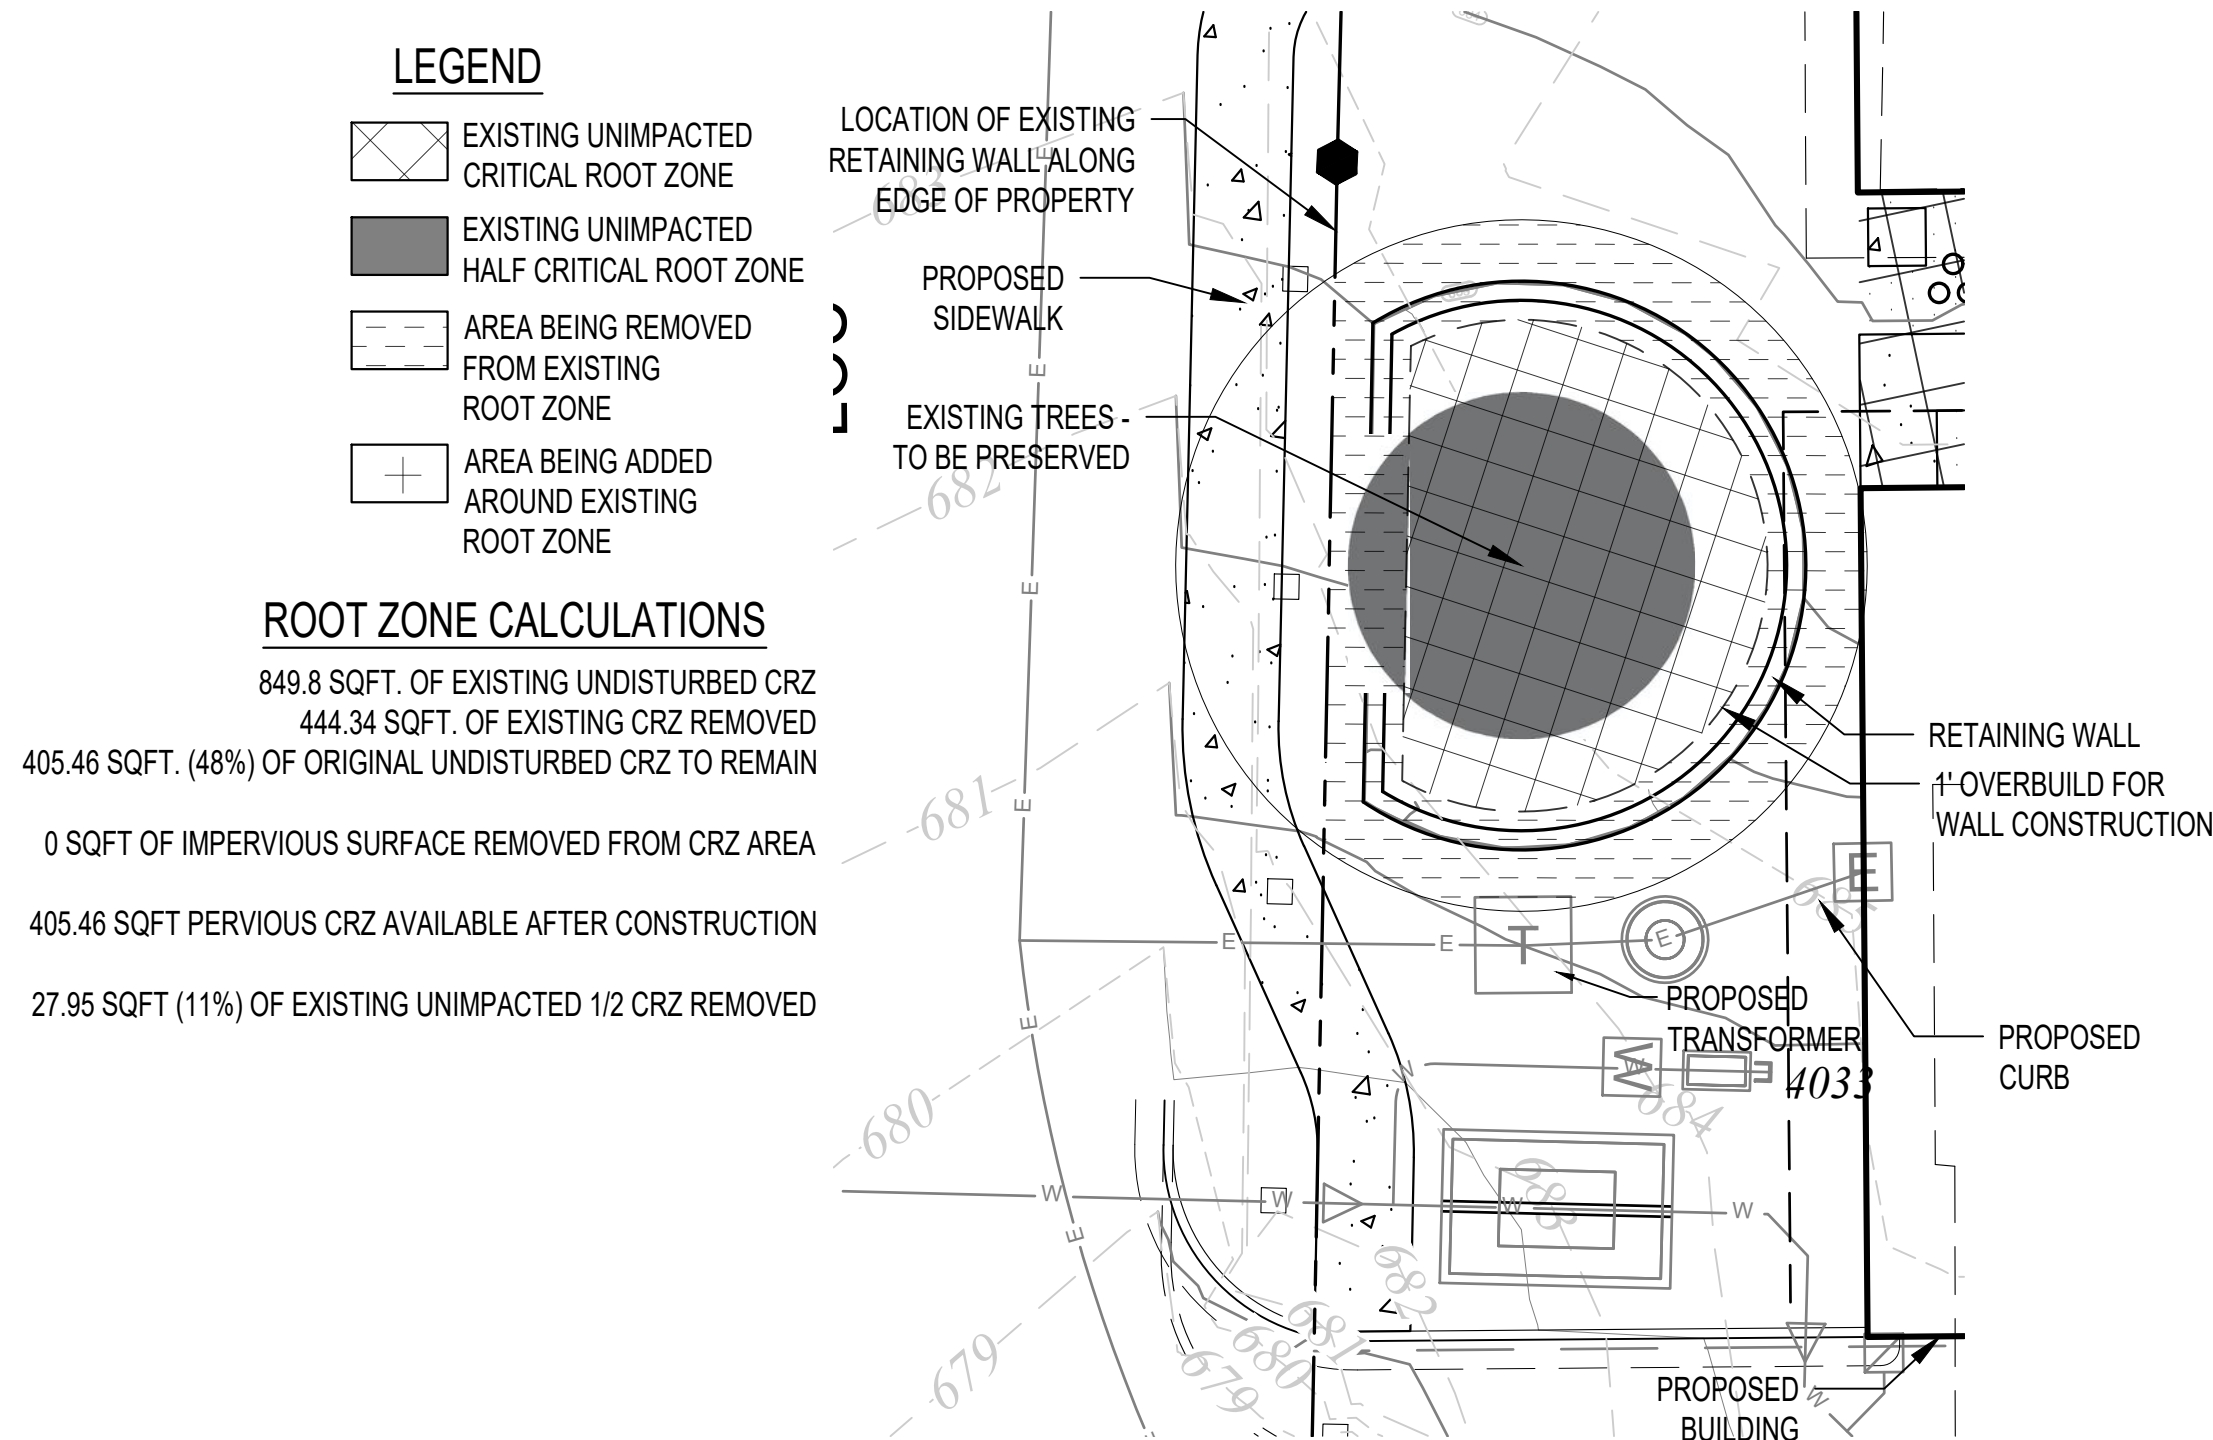

1 CRITICAL ROOT ZONE IMPACT TREE 4034

Scale: 1" = 10'-0"