
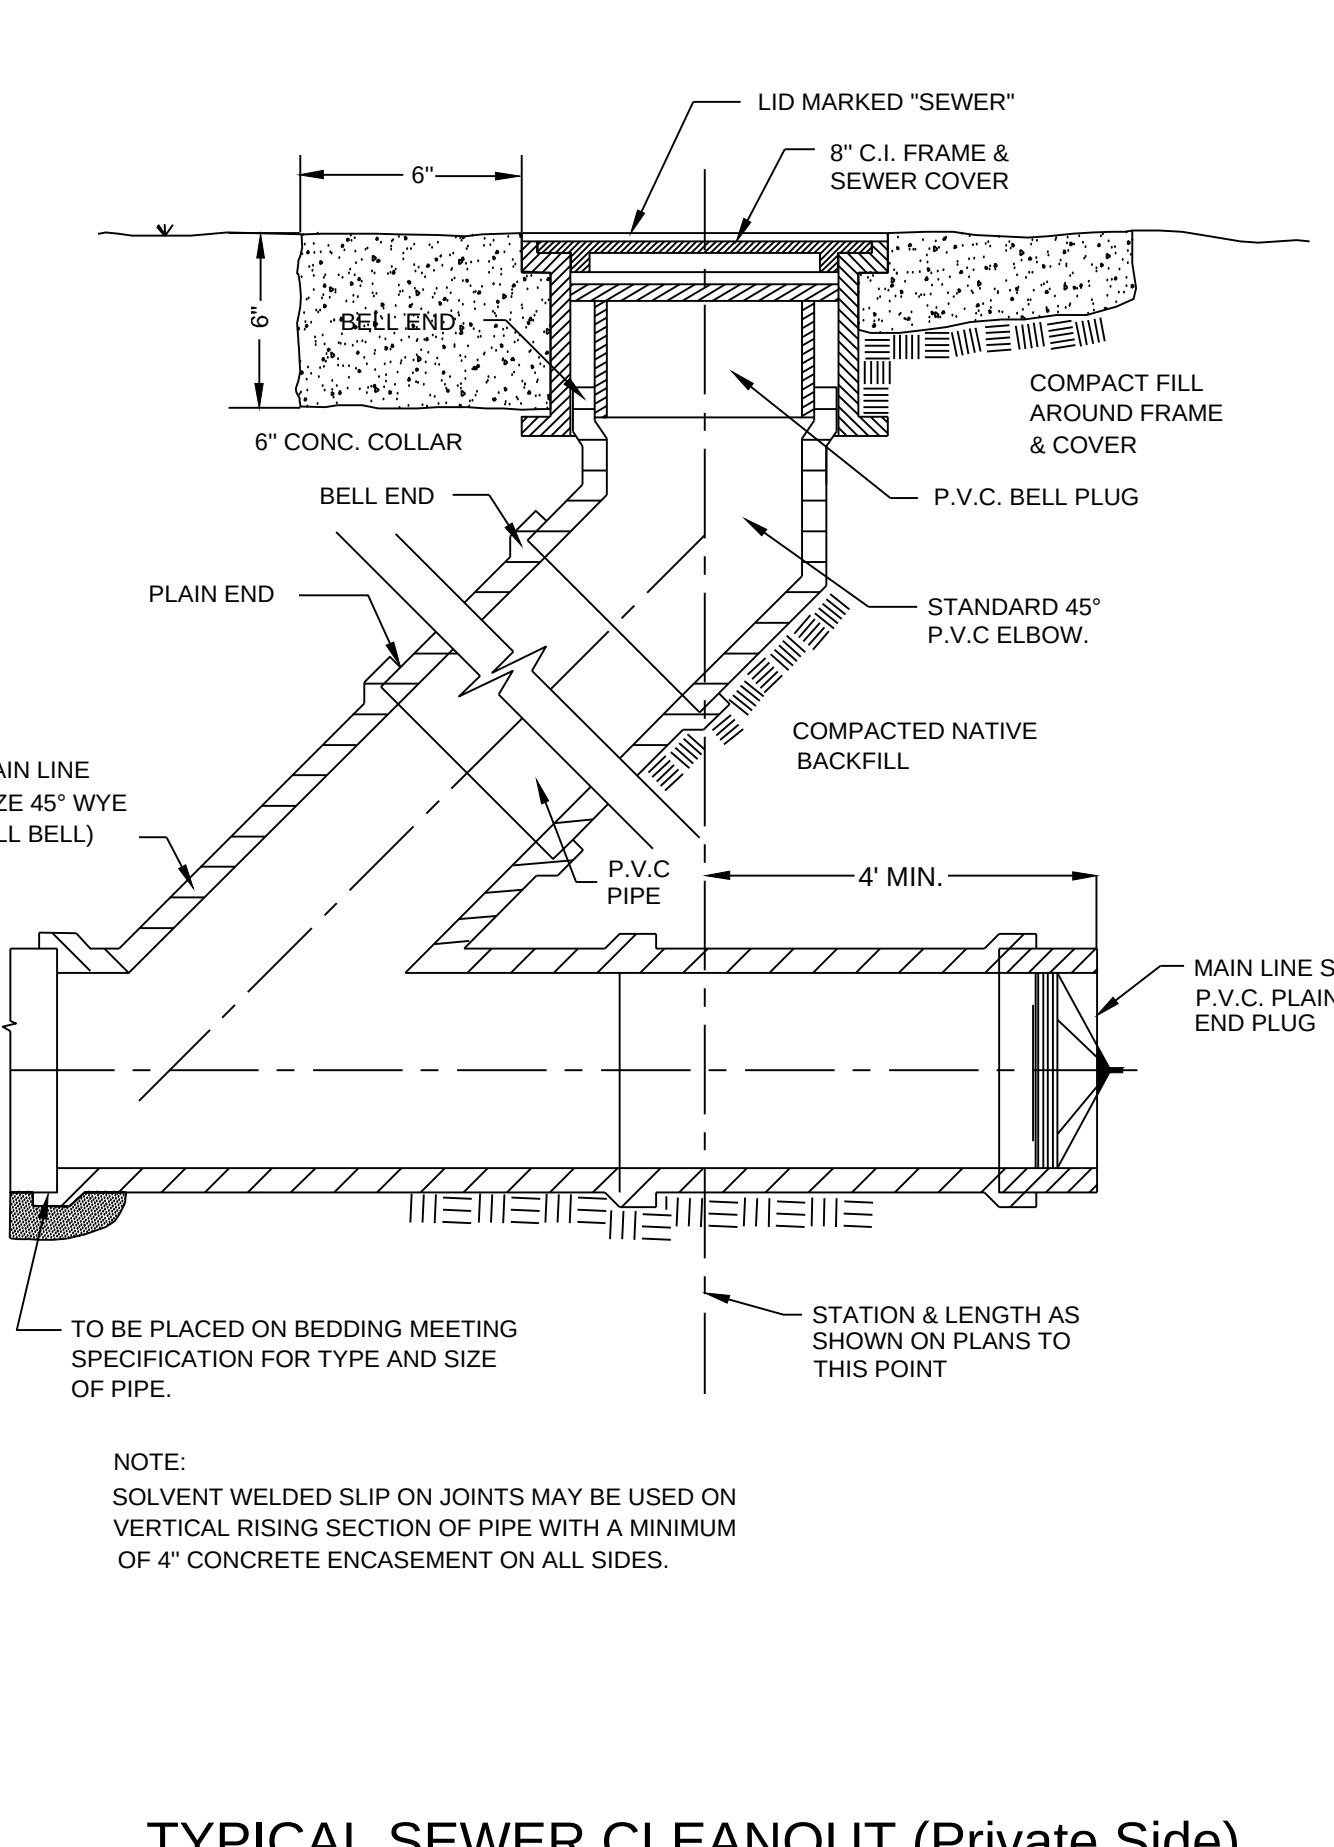
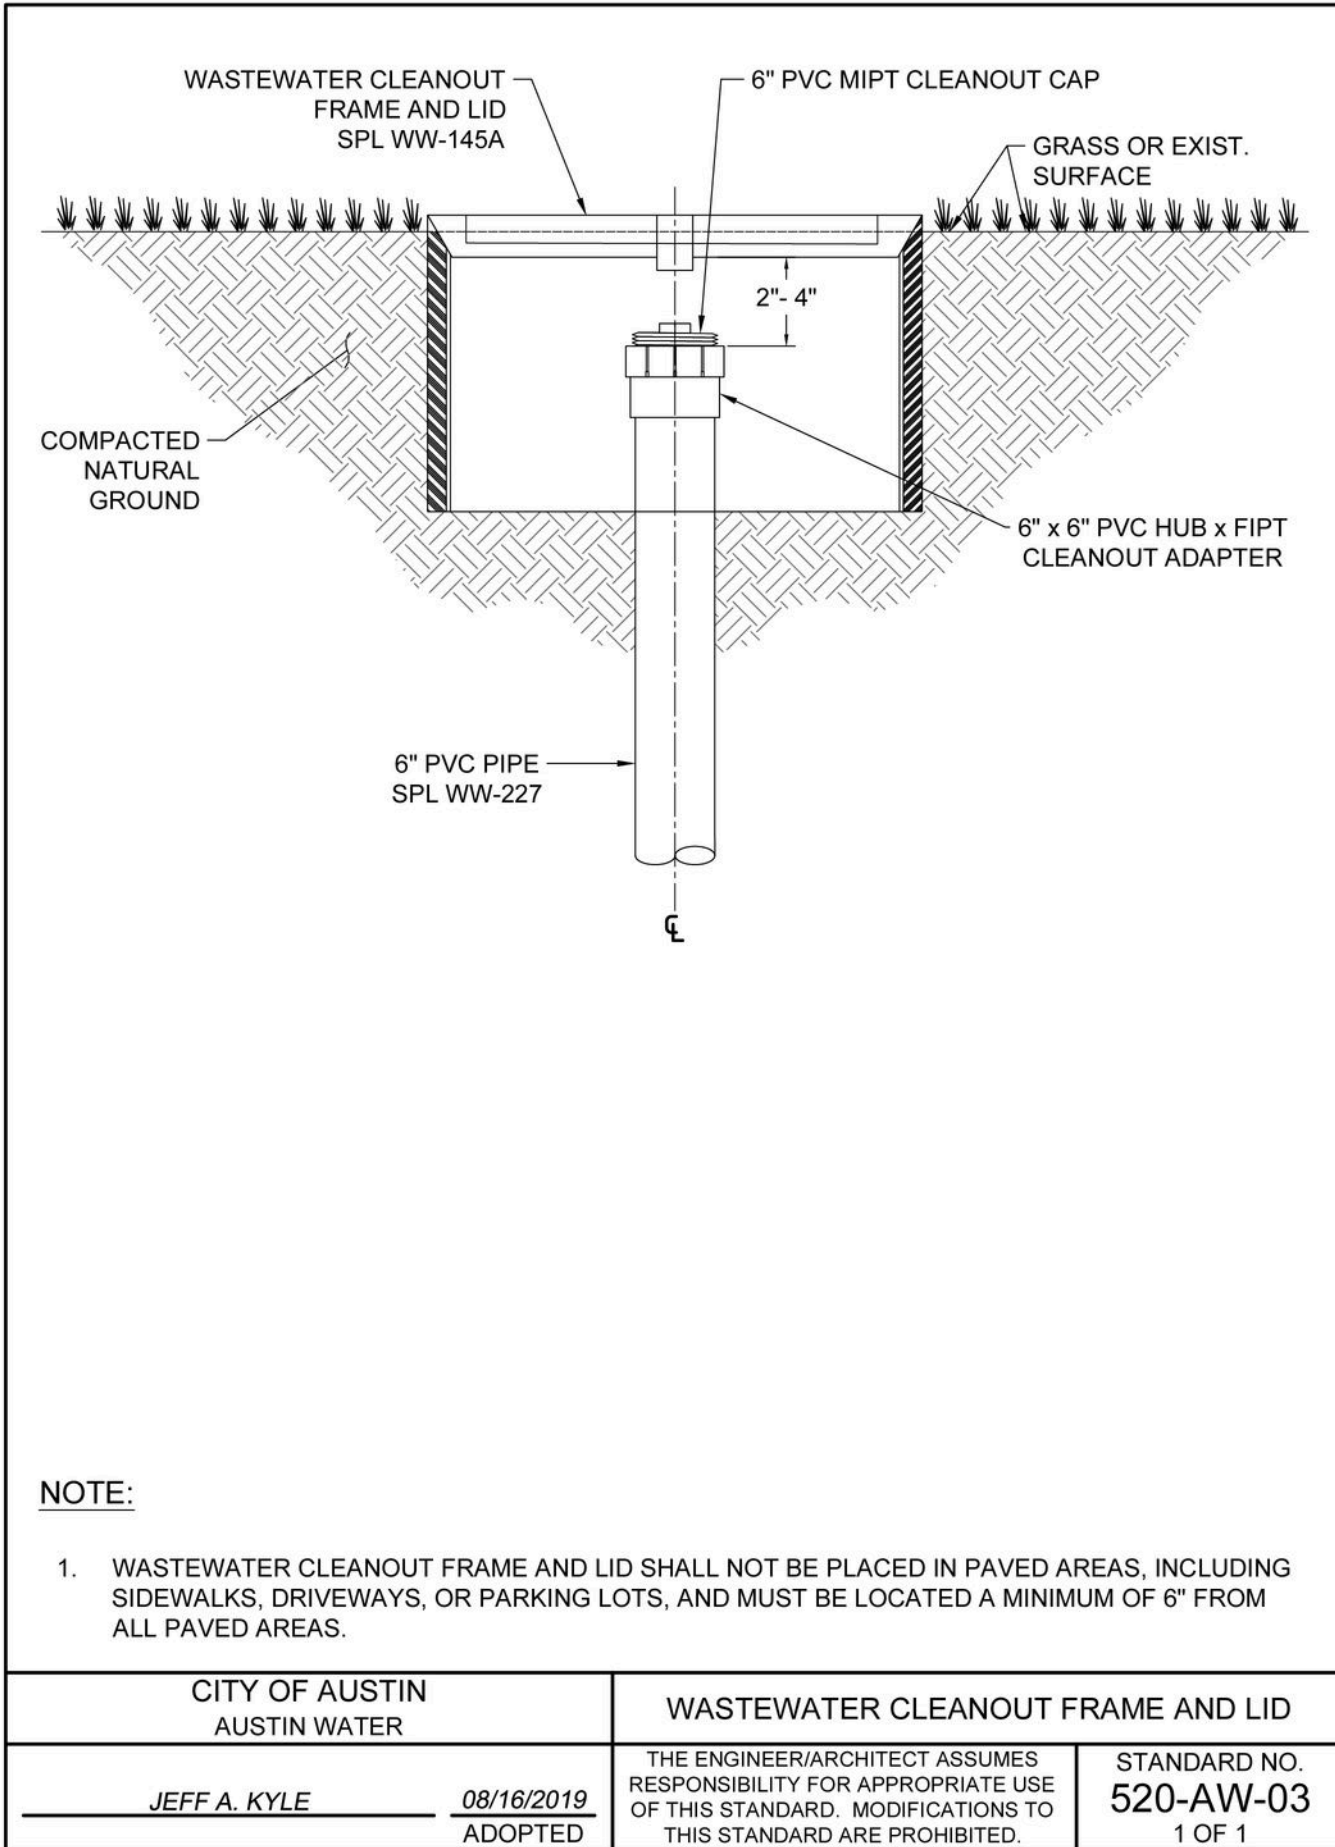
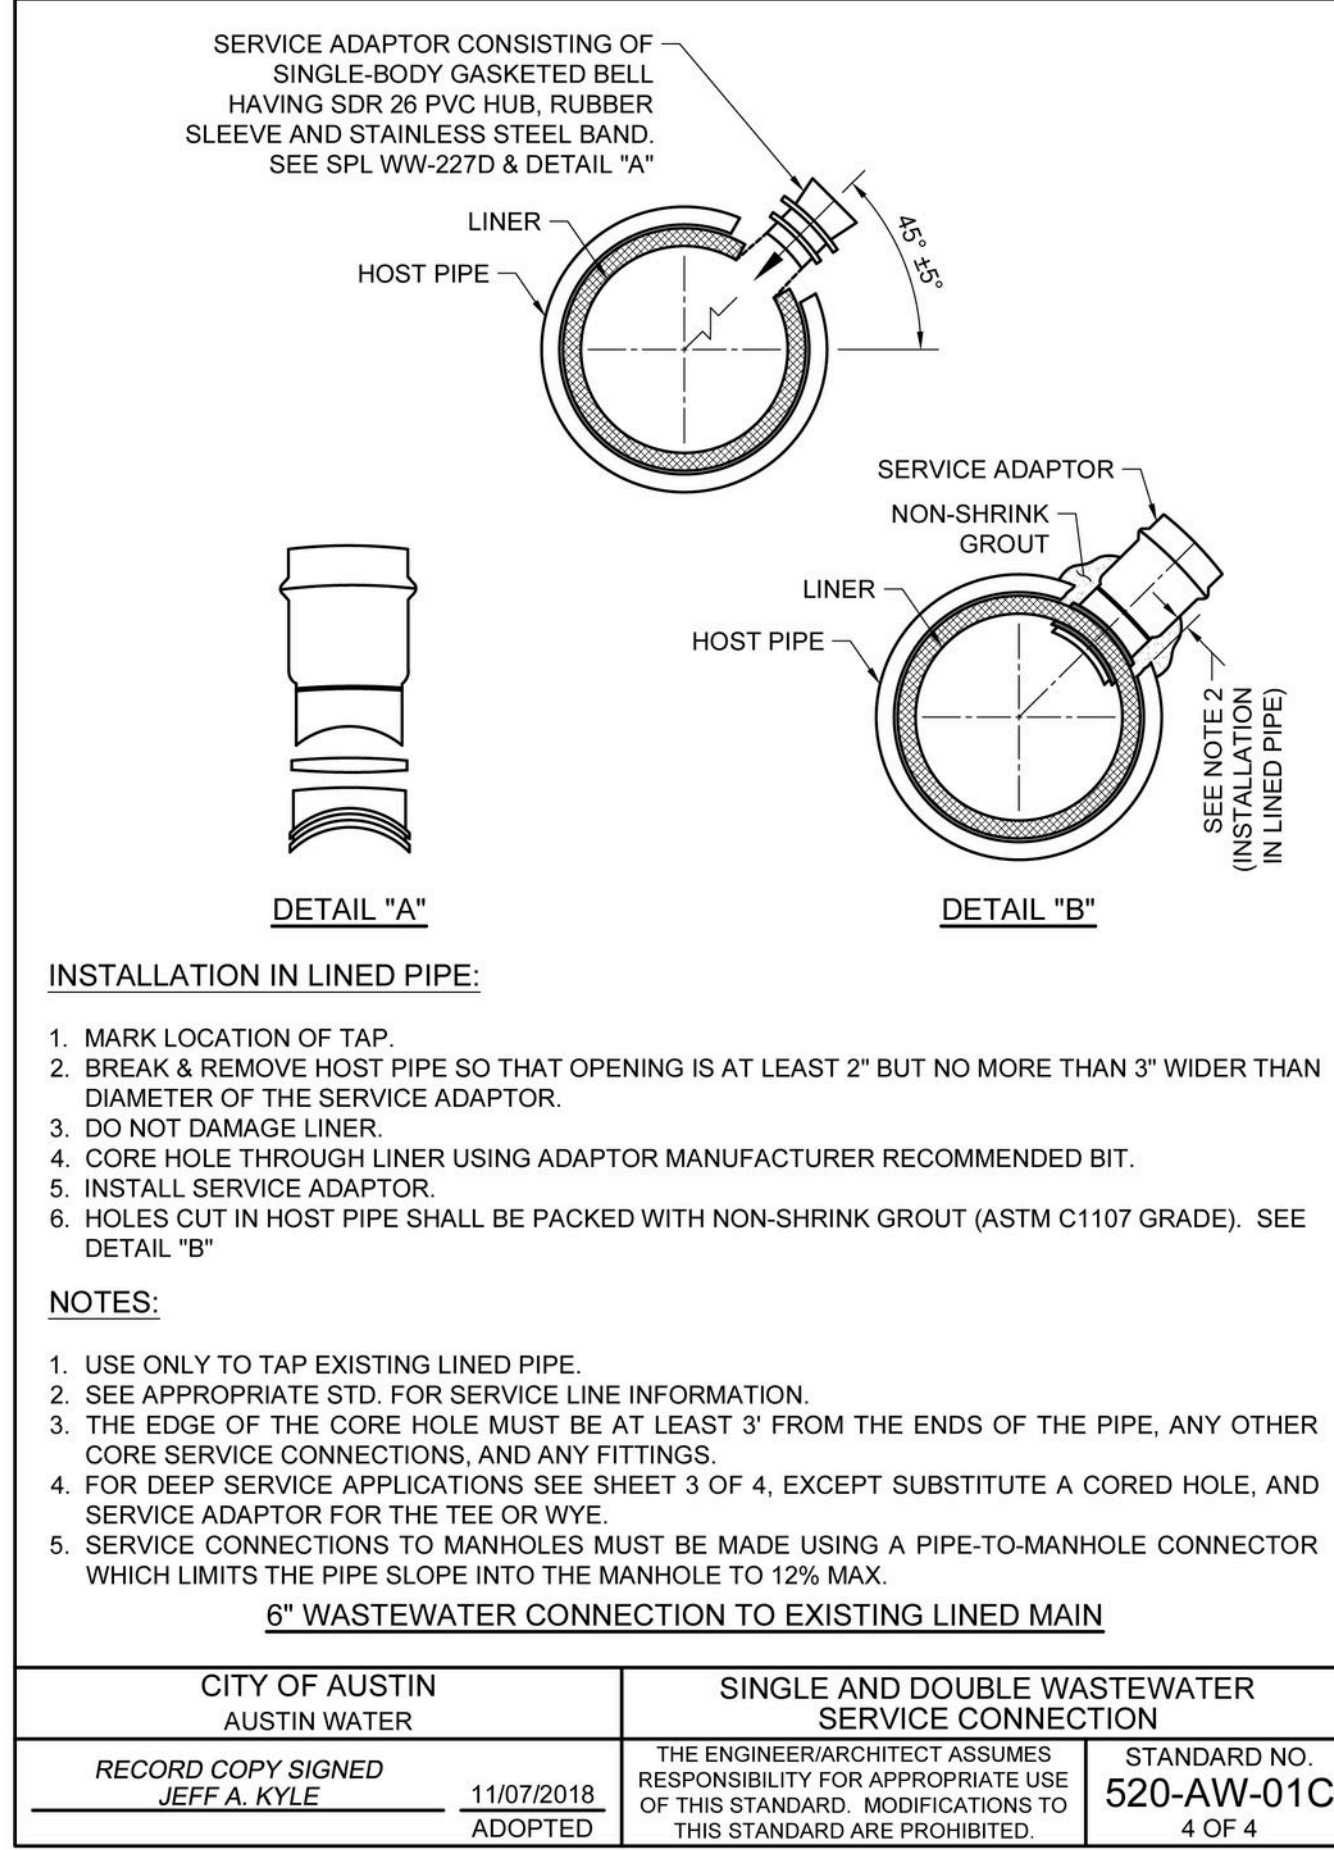
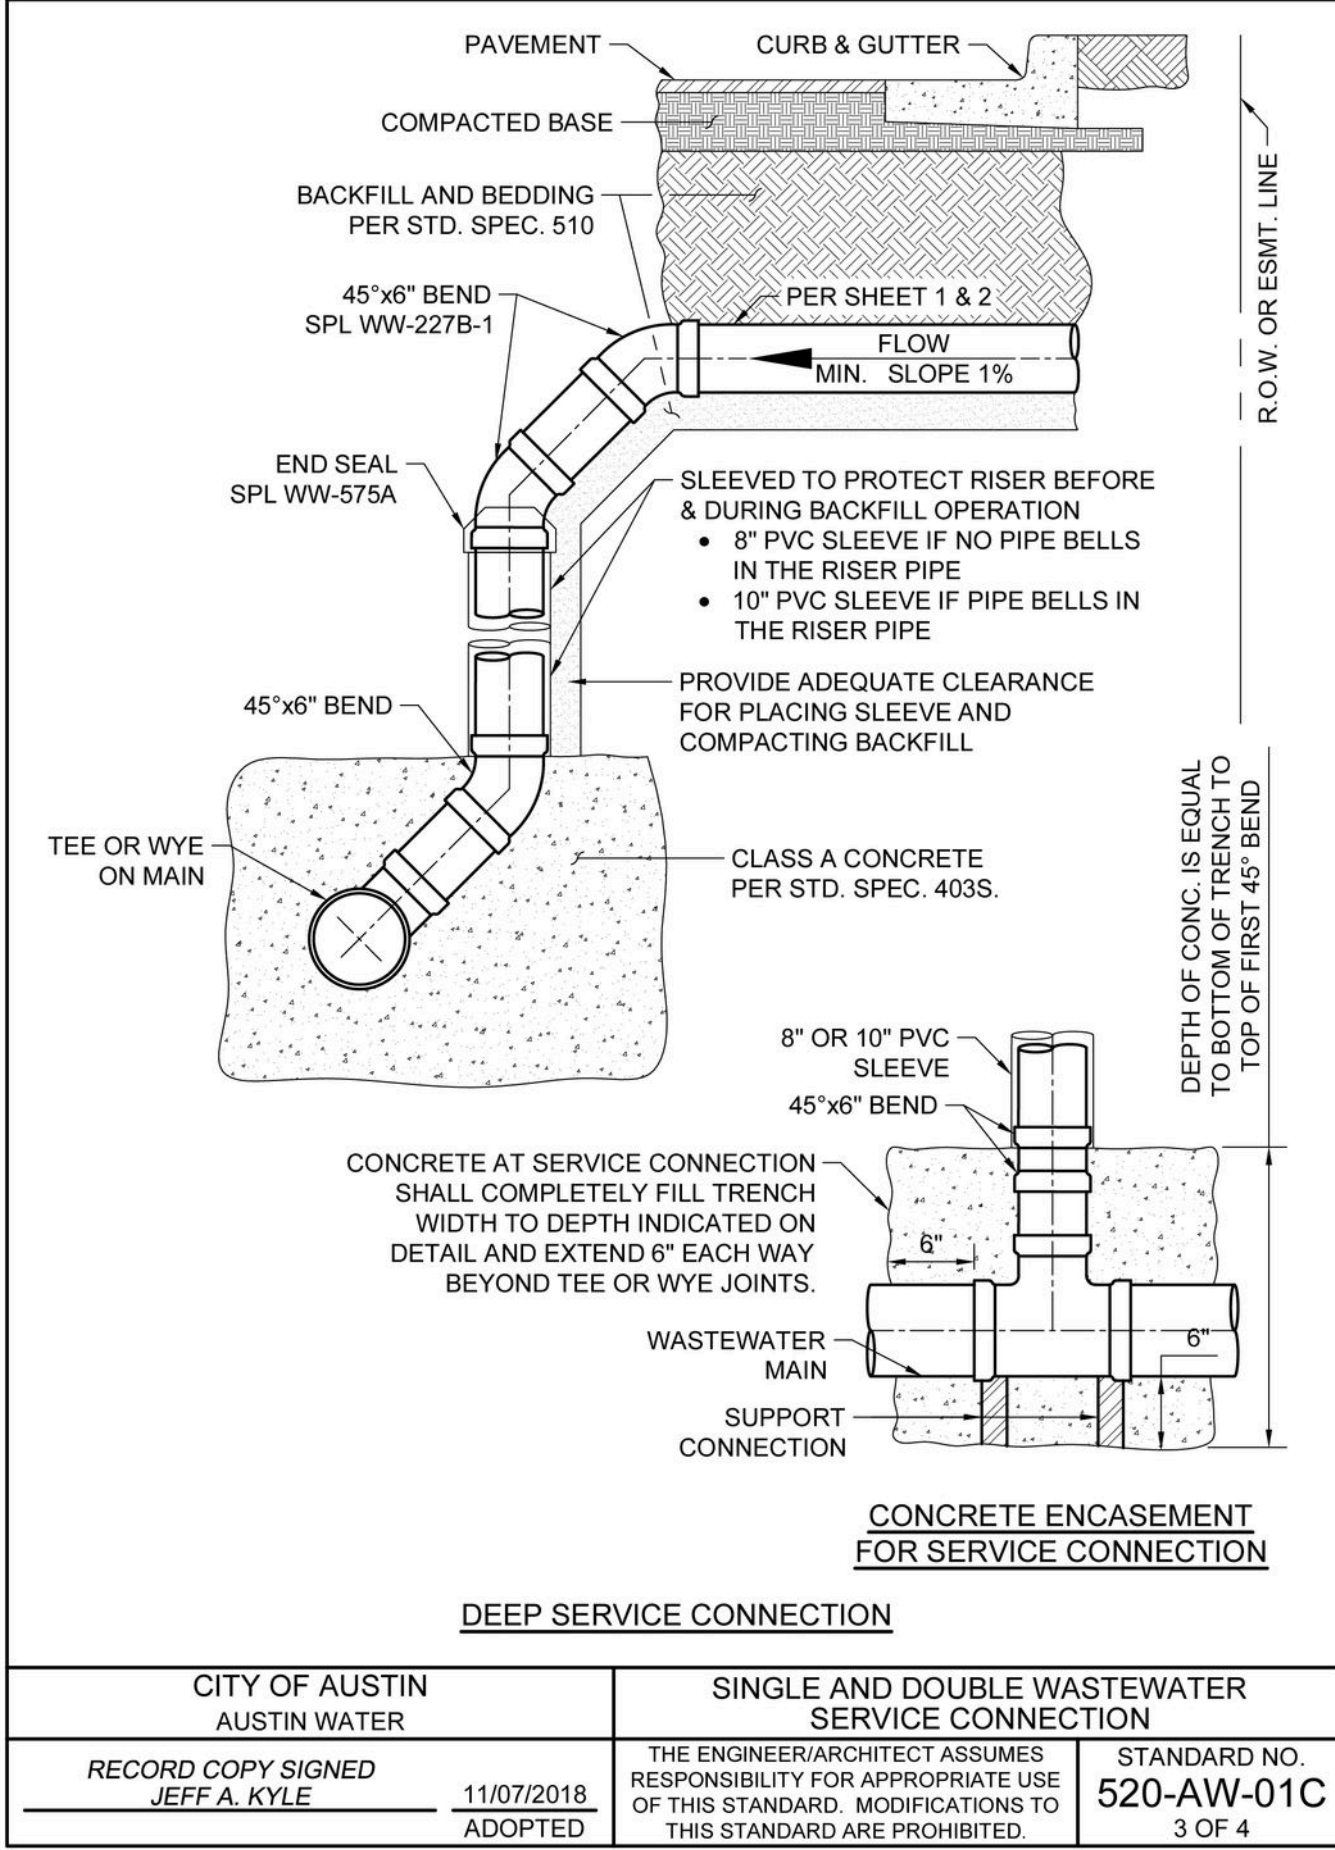
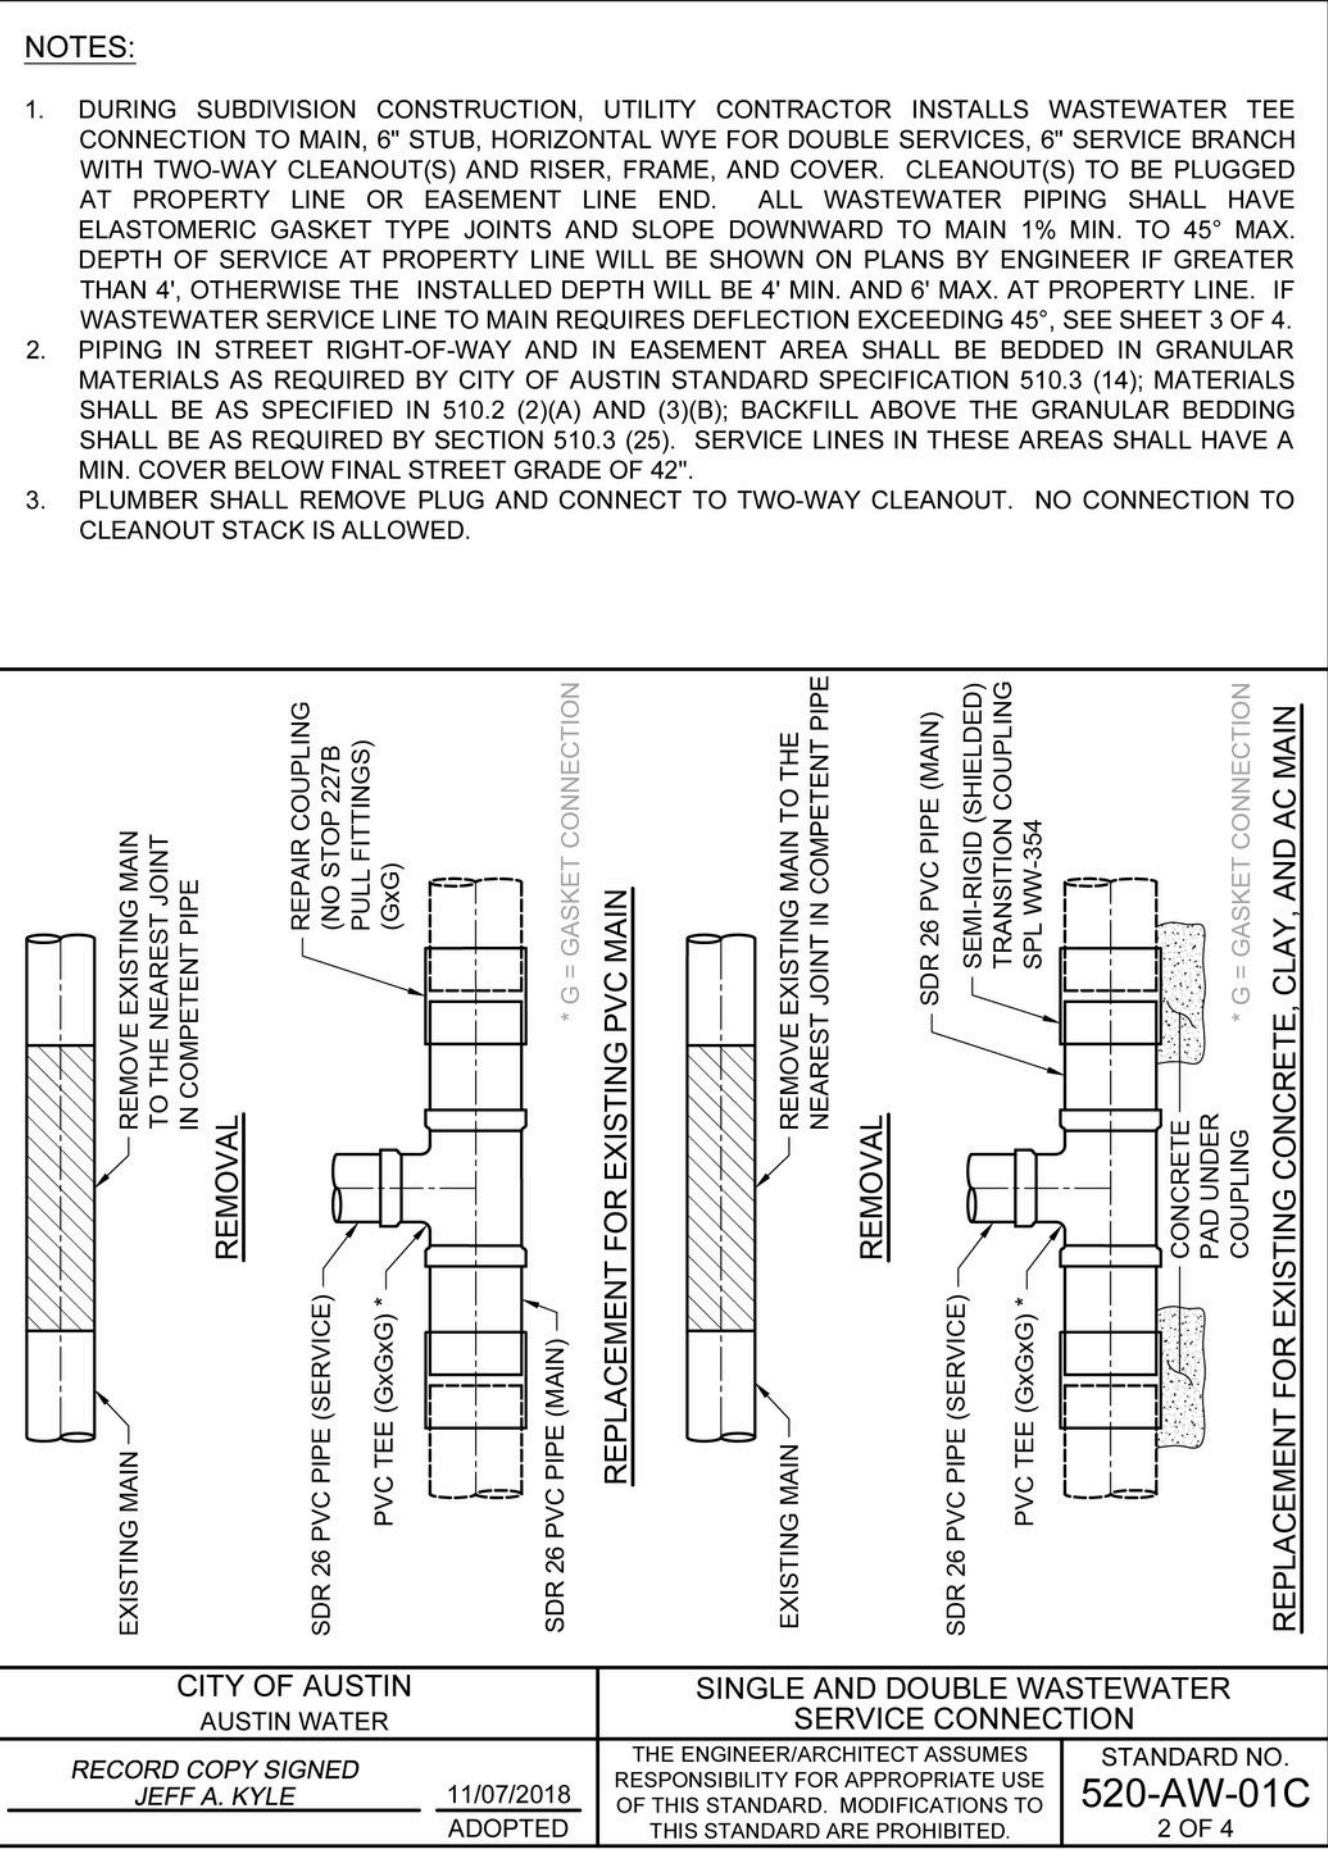


ORIGINAL LAYOUT SIZE: 24x36

©2026 H:\JOBFILES\RJ3\RJ33 BUILDING GROUP\RJ3 70496 VALLEY VIEW TOWNHOMES SP\04 CAD\PILOT SHEETS\DETAILS.DWG 2/27/2026 10:11 AM Chris Shilleesh

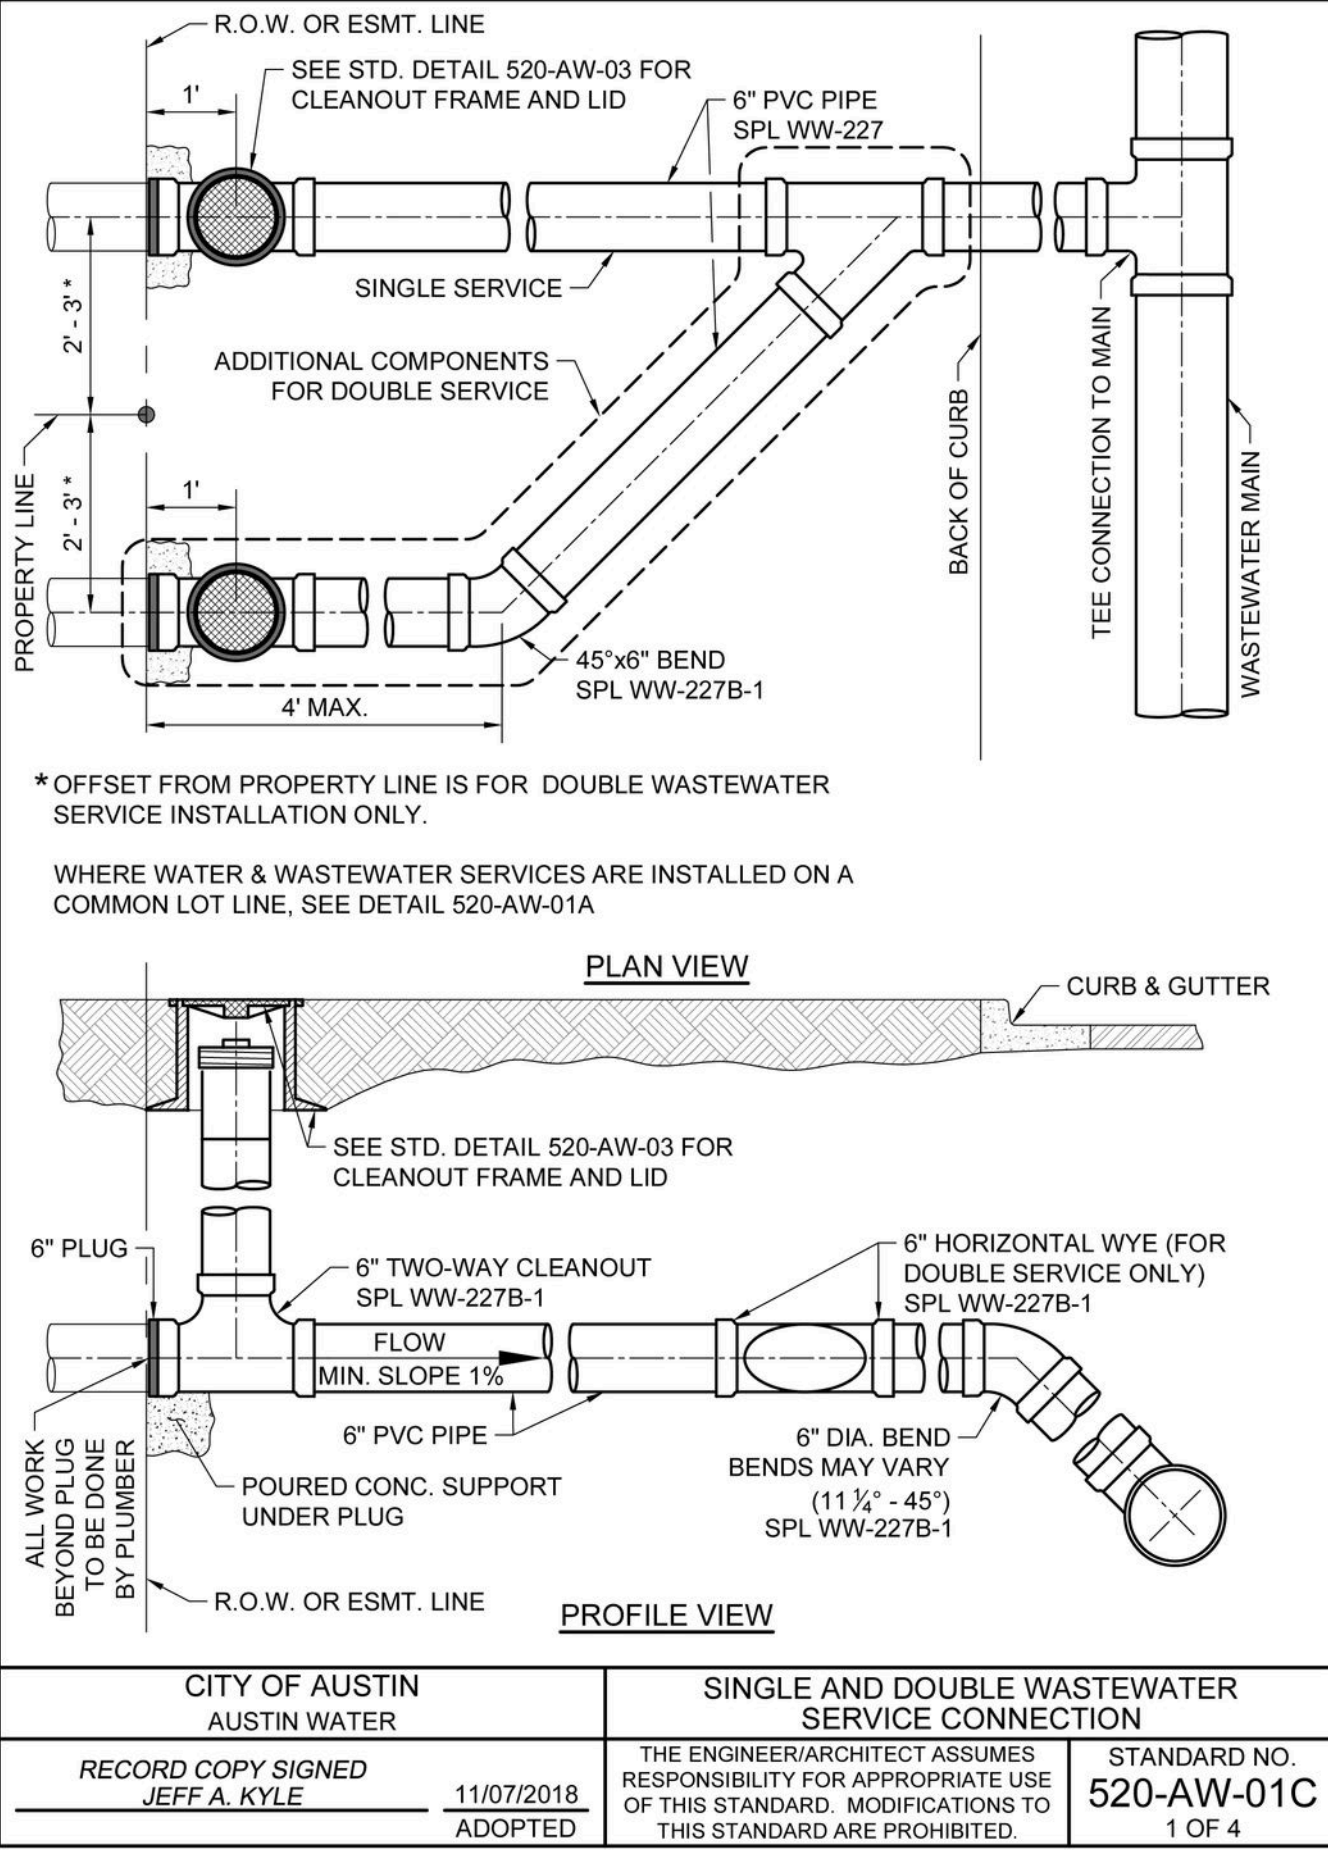

Bleyl Engineering

Planning • Design • Management
7701 San Felipe Blvd., Suite 200, Austin TX 78729
Texas Firm Registration No. F-678
Tel. 512-454-2400
www.bleylengineering.com

Construction Details 5

Valley View Townhomes
3759 Valley View Road
Austin, Texas 78704
Travis County



Design: CS, JR
CAD: JW, CS | Review: JKR
Project No: RJ3 70496
Sheet: **26** of **39**
SP-2025-0126C