


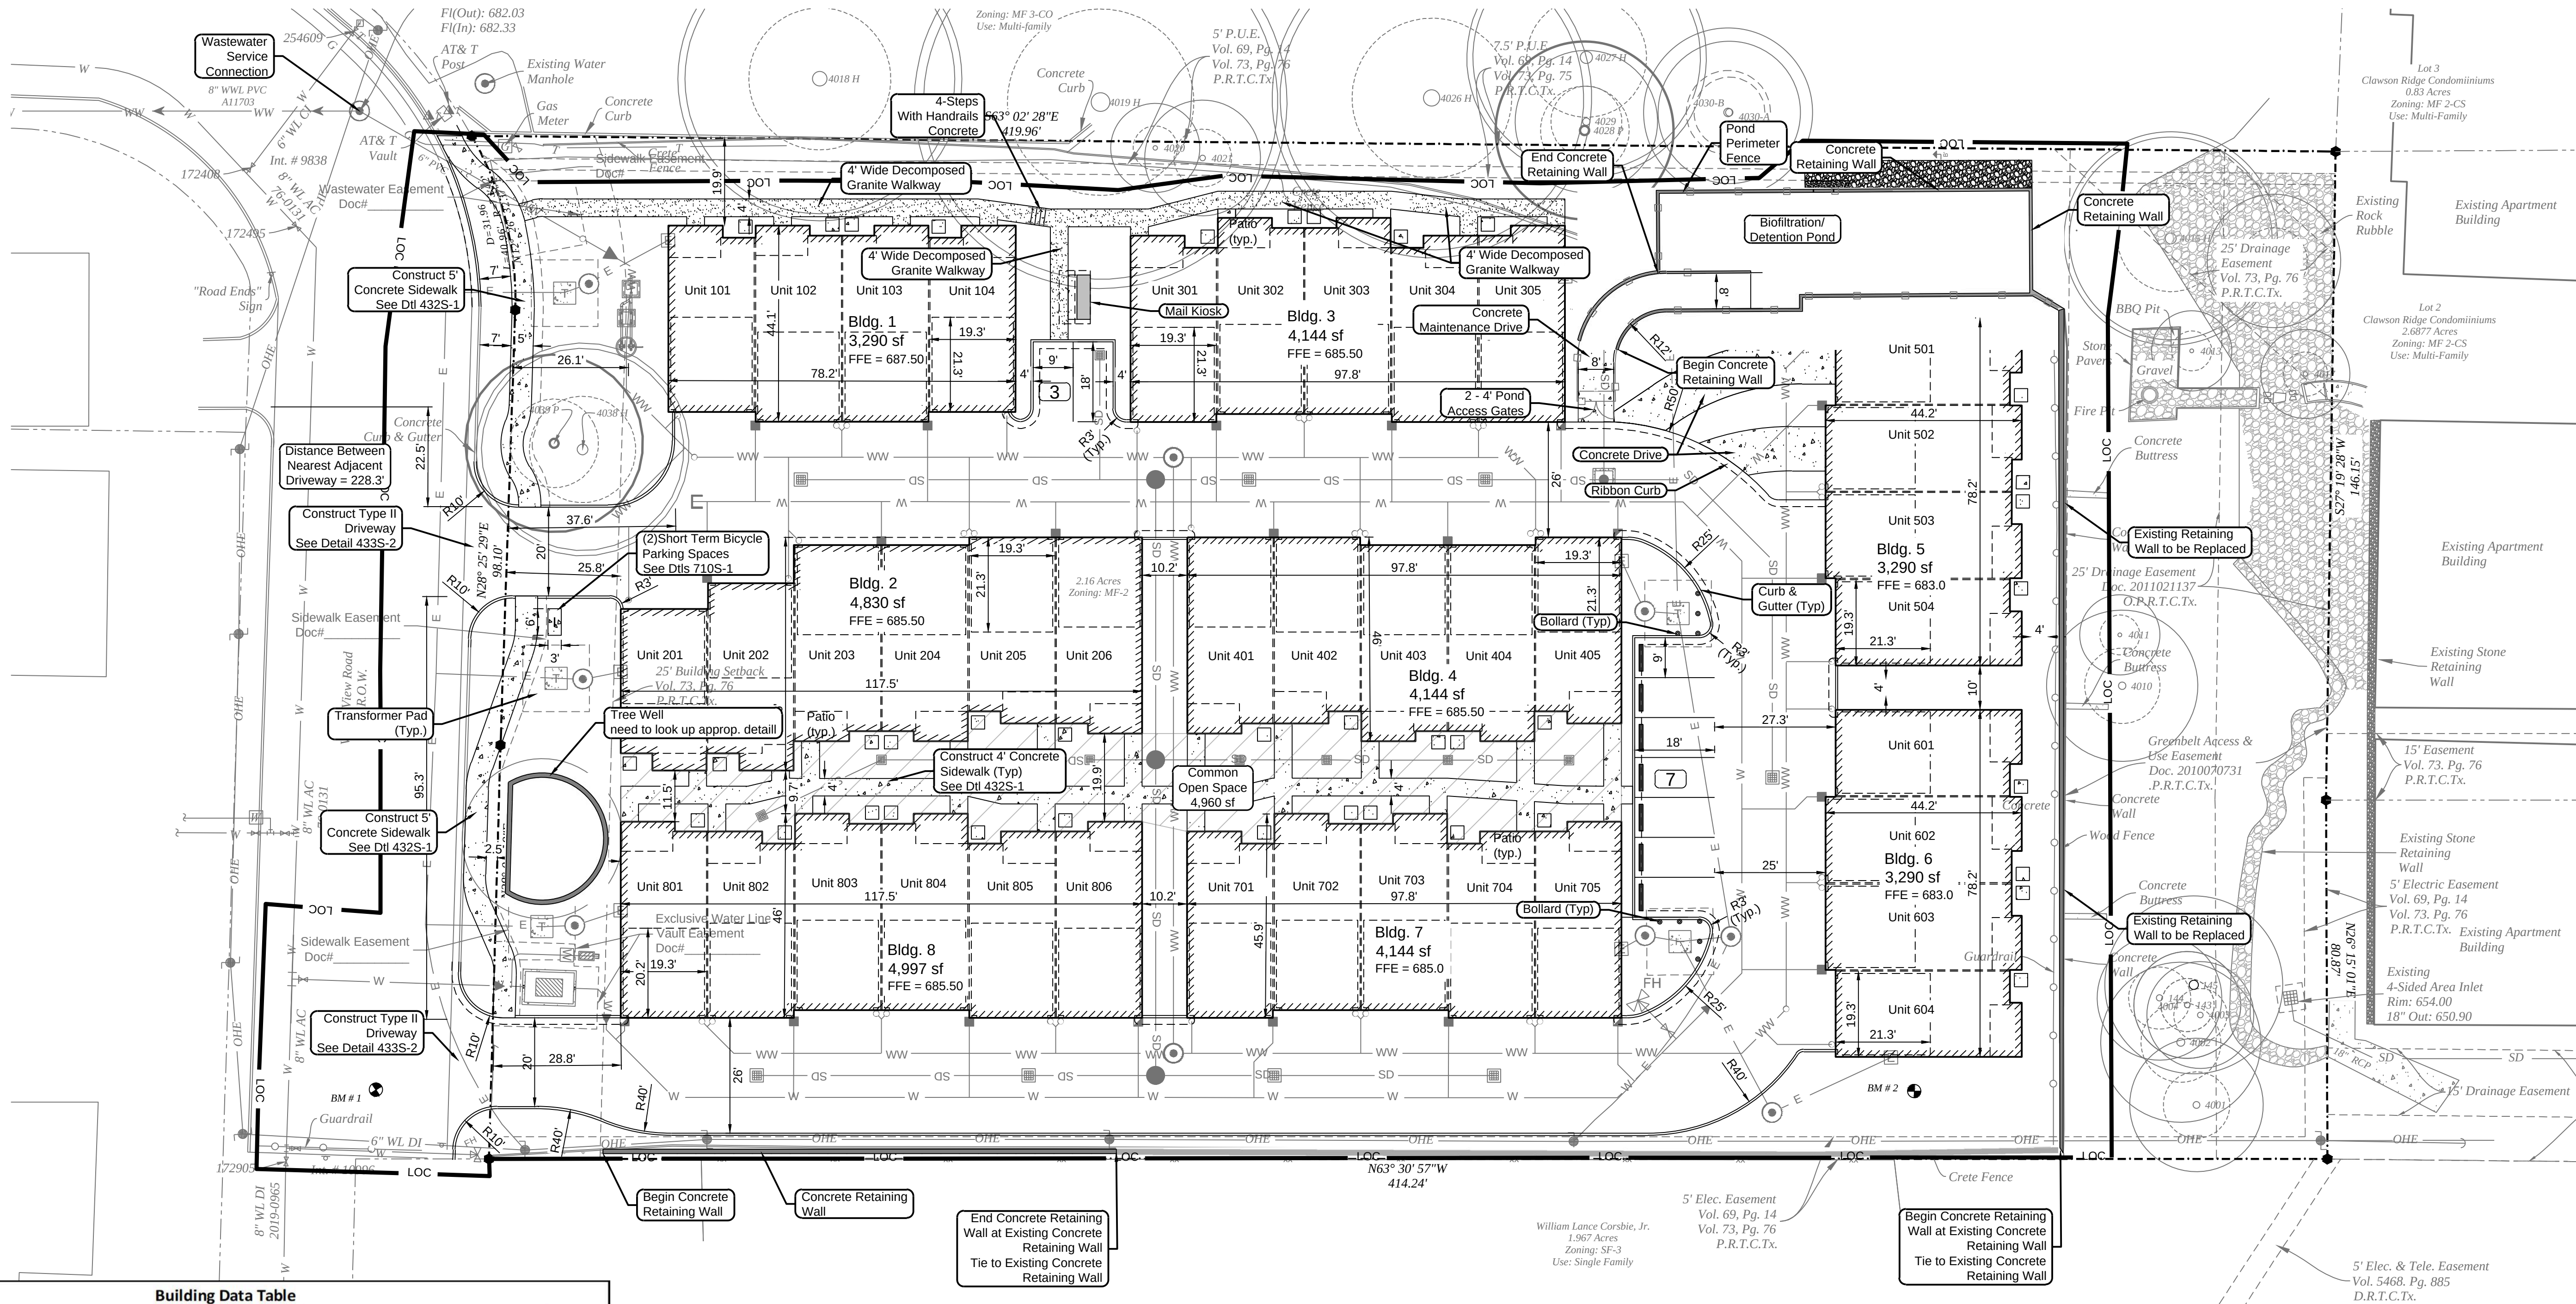

Building Data Table					
Building #	Building Type	Gross Floor Area (sf)	Building Coverage (sf)	Bedroom Type	Units
1	4 Plex	8,550	3,290	Two Bedroom	16
2	6 Plex	13,004	4,997	Three Bedroom	23
3	5 Plex	10,776	4,144	Total Units	39
4	5 Plex	10,776	4,144	Maximum Number of Building Stories = 3	
5	4 Plex	8,550	3,290		
6	4 Plex	8,550	3,290		
7	5 Plex	10,776	4,144		
8	6 Plex	13,004	4,997	Foundation = Slab on grade	

Site Area Calculation (MF-2)			
Unit Type	Efficiency	1 Bedroom	2+ Bedroom
Number of Units	0	0	39
Required Site Area Per Unit (sf)	1,600	2,000	2,400
Site Area Required (sf)	0	0	93,600
Total Site Area Required (sf)		93,600	
Total Site Area Provided (sf)		94,192	

Building #	Building Type	Average (MSL)	Building Height (FT)	Avg. Building Height (MSL)	Height Allowed (FT)	Height Allowed (MSL)
1	4 Plex	686.25	35' - 10.75"	722.15	40'	726.25
2	6 Plex	684.50	33' - 4.75"	717.90	40'	724.50
3	5 Plex	685.00	36' - 1"	721.08	40'	725.00
4	5 Plex	684.25	33' - 4.75"	717.65	40'	724.25
5	4 Plex	682.17	35' - 10.75"	718.07	40'	722.17
6	4 Plex	681.75	35' - 10.75"	717.65	40'	721.75
7	5 Plex	682.50	33' - 4.75"	715.90	40'	722.50
8	6 Plex	682.25	33' - 4.75"	715.65	40'	722.25

Zoning:	MF-2/Multi-Family Low Density		
Use: Multi-Family Residential	s.f.	acres	%
Site Area:	94,192	2.162	
Allowable Impervious Cover:	56,515	1.297	60%
Existing Impervious Cover:	61,350	1.408	65%
Impervious Cover Removed:	61,350	1.408	65%
Total Impervious Cover:	55,502	1.274	59%
Allowable Building Coverage:	47,096	1.081	50%
Proposed Building Coverage:	32,296	0.741	34%
Gross Floor Area:	83,986	1.928	
Building Slab Construction	Slab On Grade		
Common Open Space Required	4709.62		
Common Open Space provided	4710		

Site Plan Release Notes

- a. All improvements shall be made in accordance with the released site plan. Any additional improvements will require site plan amendment and approval of the Development Services Department.
- b. Approval of this Site Plan does not include Building and Fire Code approval nor building permit approval.
- c. All signs must comply with requirements of the Land Development Code ([Chapter 25-10](#)).
- d. Additional electric easements may be required at a later date.
- e. Water and wastewater service will be provided by the City of Austin (or identify the service provider if other than the City of Austin).
- f. All existing structures shown to be removed will require a demolition permit from the City of Austin Development Services Department.
- g. No certificate of occupancy may be issued for the proposed residential condominium project until the owner or owners of the property have complied with Chapter 81 and 82 of the Property Code of the State of Texas or any other statutes enacted by the State concerning condominiums.
- h. For driveway construction: The owner is responsible for all costs for relocation of, or damage to utilities.
- i. For construction within the right-of-way, a ROW excavation permit is required.

Lighting Note

All exterior lighting will be full cut-off and fully shielded in compliance with Subchapter E 2.5. All site lighting to be located on the building will be in compliance with Subchapter E 2.5, and will be reviewed during building plan review. Any change or substitution of lamps/light fixtures shall be submitted to the Director for approval in accordance with Section 2.5.2.E. See Figure 34.

Trash Collection Notes

- Trash containers shall not be left at curb side unattended. Signs must be posted on the building or at a location that is publicly visible indicating that trash containers may not be left at curbside. The sign shall indicate the City of Austin's Code enforcement phone number for the public to report violations.
- A restrictive covenant may be required for enforcement purposes.

Reference: TCM, 9.4.2

Accessibility Notes

1. Approval of these plans by the City of Austin indicates compliance with applicable City regulations only. Compliance with accessibility standards such as the 2010 Standards for Accessible Design or the 2012 Texas Accessibility Standards was not verified. The applicant is responsible for compliance with all applicable accessibility standards.
2. Accessible parking spaces must be located on a surface with a slope not exceeding 1:50.
3. Accessible routes must have a cross-slope no greater than 1:50.
4. Slopes on accessible routes may not exceed 1:20 unless designed as a ramp.
5. The maximum slope of a ramp in new construction is 1:12. The maximum rise for any ramp is 20in. The maximum horizontal projection is 30 feet for a ramp with a slope between 1:12 and 1:15, and 40 feet for a ramp with a slope between 1:16 and 1:20.

Benchmarks

B.M. #1 - Mag Nail Set in Asphalt
Elevation = 678.52' NAVD 88 (GEOID 18)

B.M. #2 - Mag Nail Set in Asphalt
Elevation = 681.08' NAVD 88 (GEOID 18)

Legal Description
Lot 1, Mecey Subdivision Volume 73, Page 76, Plat Records of Travis County, Texas.

<u>Parking Data</u>	
Land Use	Residential
Parking Spaces Provided	10 Surface/ 78 Garage
Compact Spaces Provided	0
ADA Spaces Required	X
ADA Spaces Provided	X
Total Bicycle Spaces Required	5
Long Term Bicycle Spaces Required	3
Long Term Bicycle Spaces Provided	39 (1 per Garage)
Short Term Bicycle Spaces Required	2
Short Term Bicycle Spaces Provided	2

Fence Note

Post holes that are to be installed near a trees Critical Root Zone (CRZ) will be dug by hand. No machinery is allowed in the CRZ and any work done in this area shall be done by hand. Add a 3-inch layer of hardwood mulch in the CRZ prior to commencing construction activities.

The location of all existing utilities shown on these plans has been based upon record information only and may not match locations as constructed. The contractor shall contact Texas 811 for assistance in determining existing utility locations prior to beginning construction. Contractor shall field verify locations of utility crossings prior to beginning construction.

