


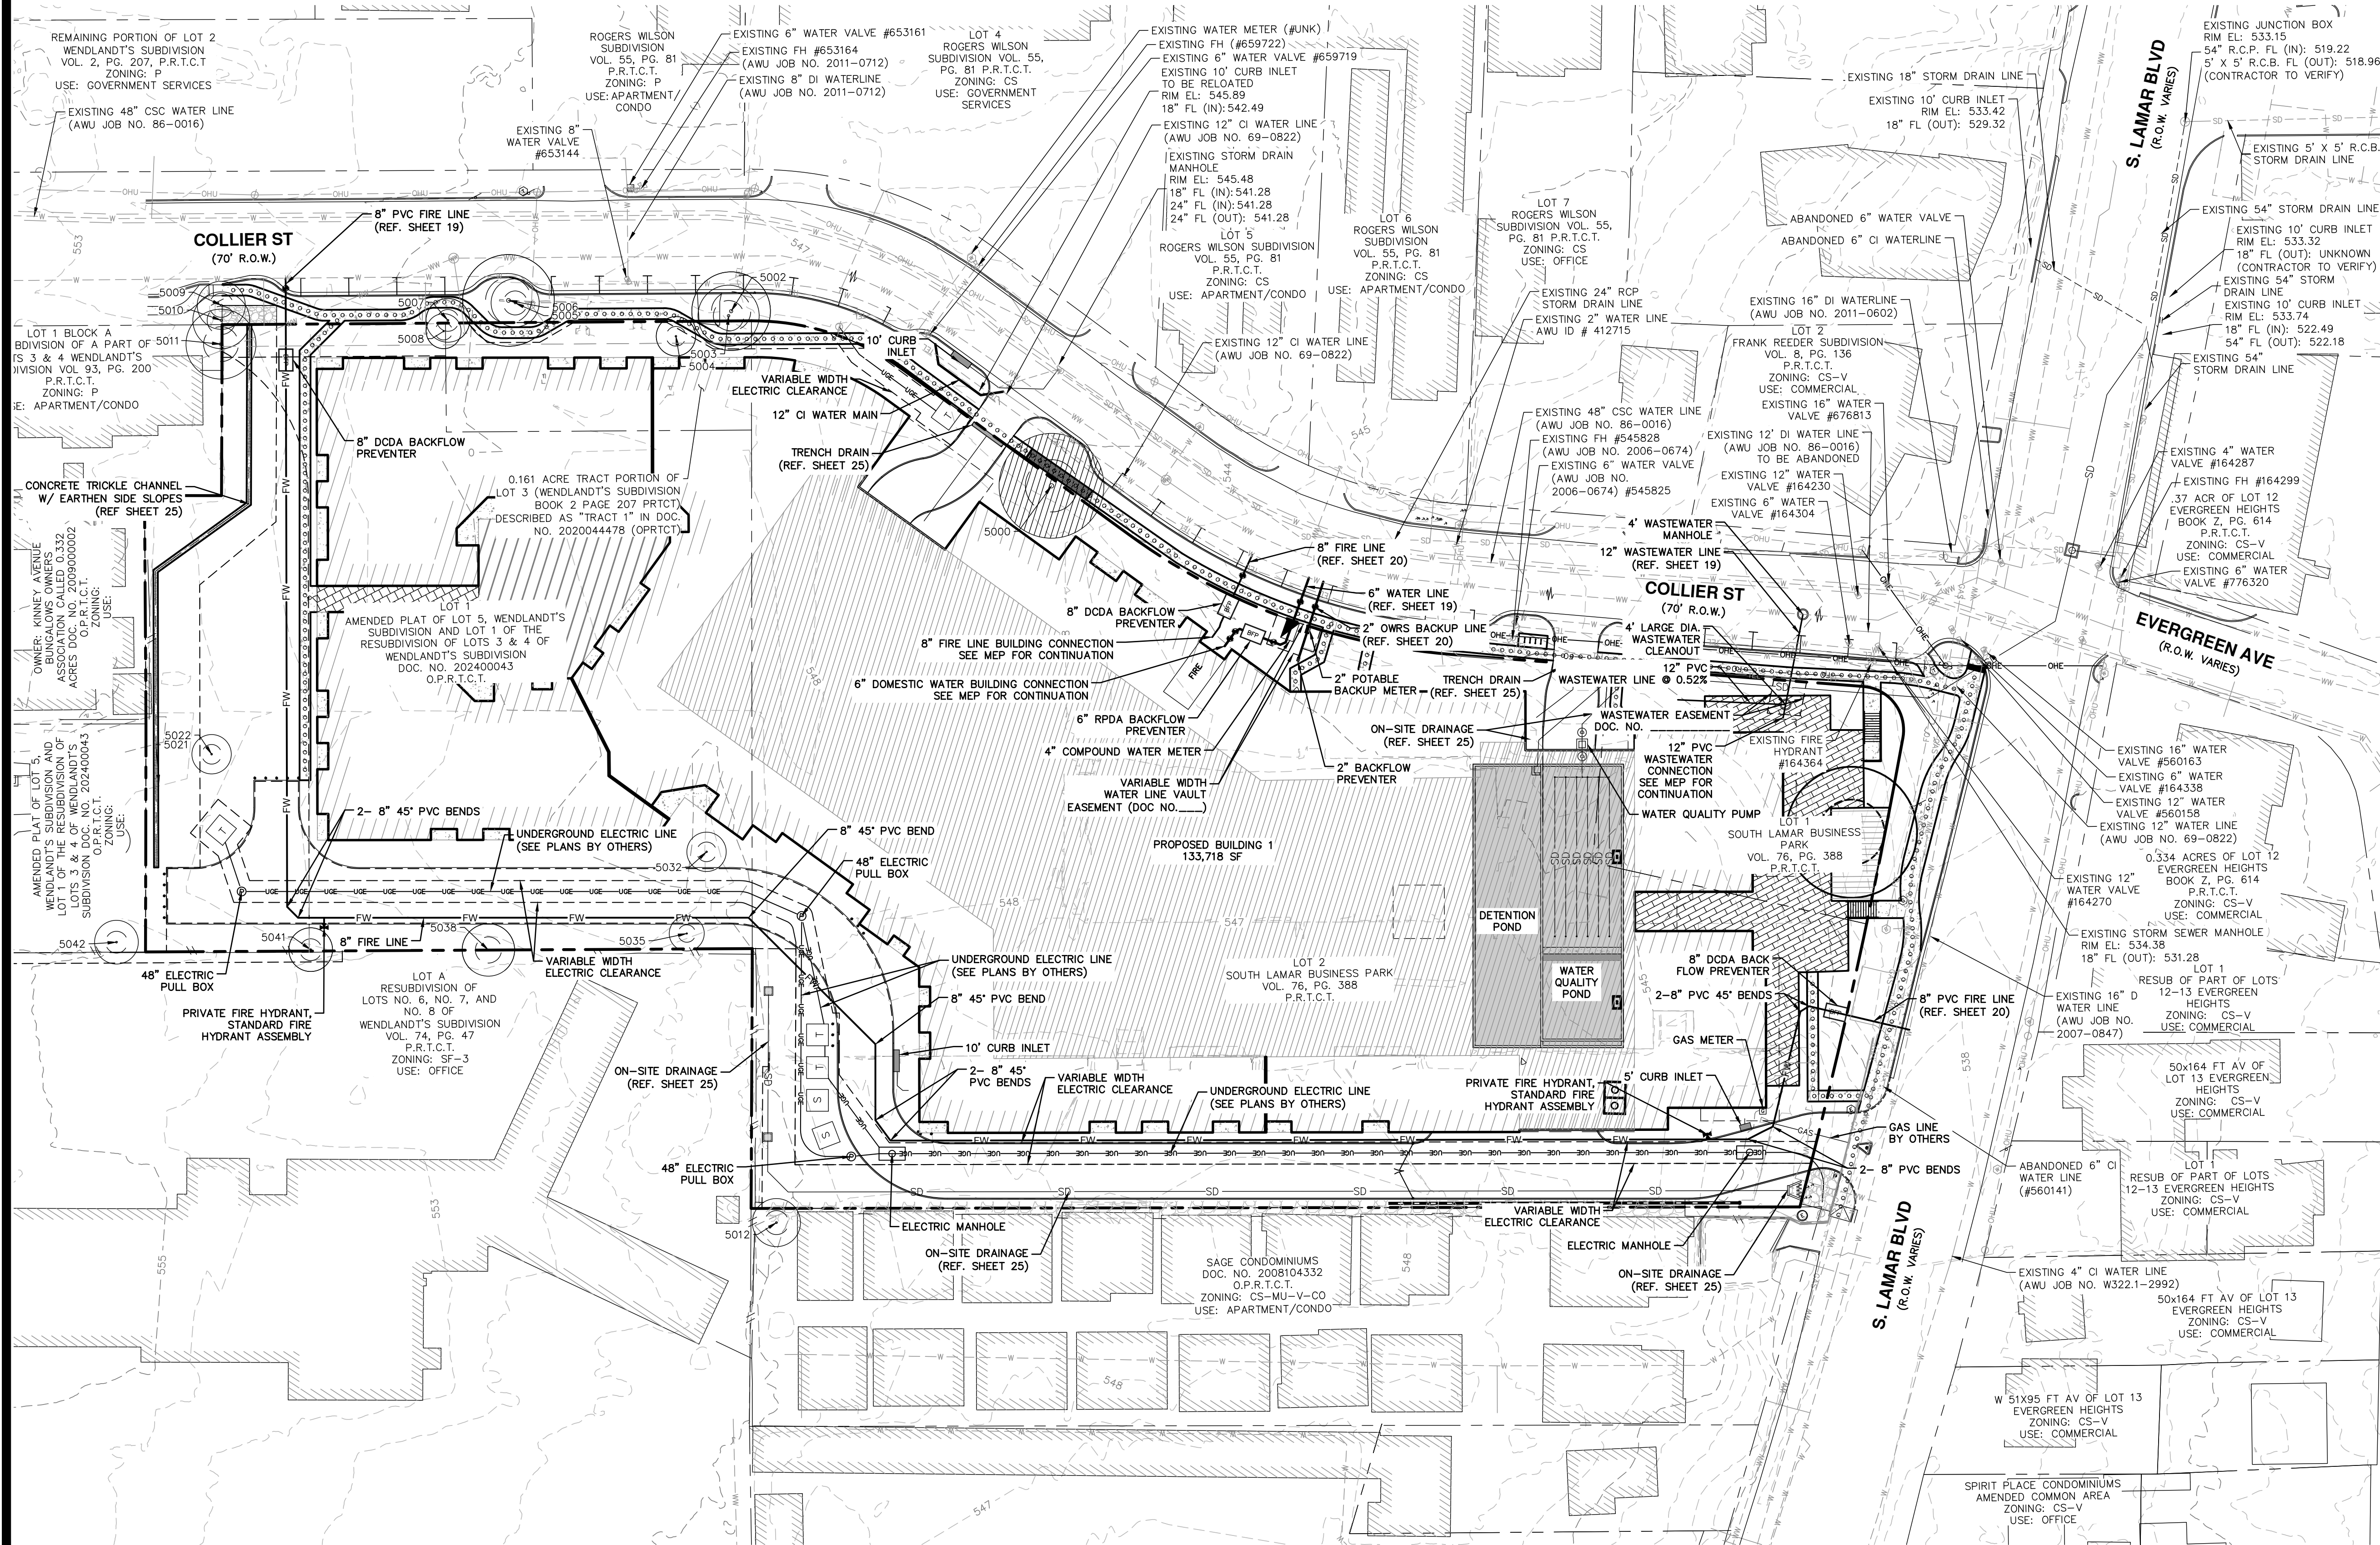

DATE: _____
NO. REVISION: _____

STATE OF TEXAS
SHelly MITCHELL
103662
PROFESSIONAL ENGINEER
04/23/2026
Shelly Mitchell

PAPE-DAWSON
10801 MOPAC EXPY, BLDG 3, STE 200 | AUSTIN, TX 78759 | 512.454.8711
TEXAS SURVEYING FIRM #4701 TEXAS SURVEYING FIRM #10028600

1700 SOUTH LAMAR
1700 SOUTH LAMAR BLVD.
AUSTIN, TEXAS 78704

PLAT NO. _____
JOB NO. 51554-00
DATE APRIL 2026
DESIGNER MW
CHECKED EAL DRAWN JLM
SHEET 18 OF 52

OVERALL UTILITY PLAN