


ORIGINAL LAYOUT SIZE - 24x36
© 2026 H:\JOBFILES\13\13.13 BUILDING GROUP\13.13 VALLEY VIEW TOWNHOMES SP\04 CAD\PILOT SHEET\STORM SEWER PLAN.DWG 2/27/2026 10:09 AM Chris Shalsheth

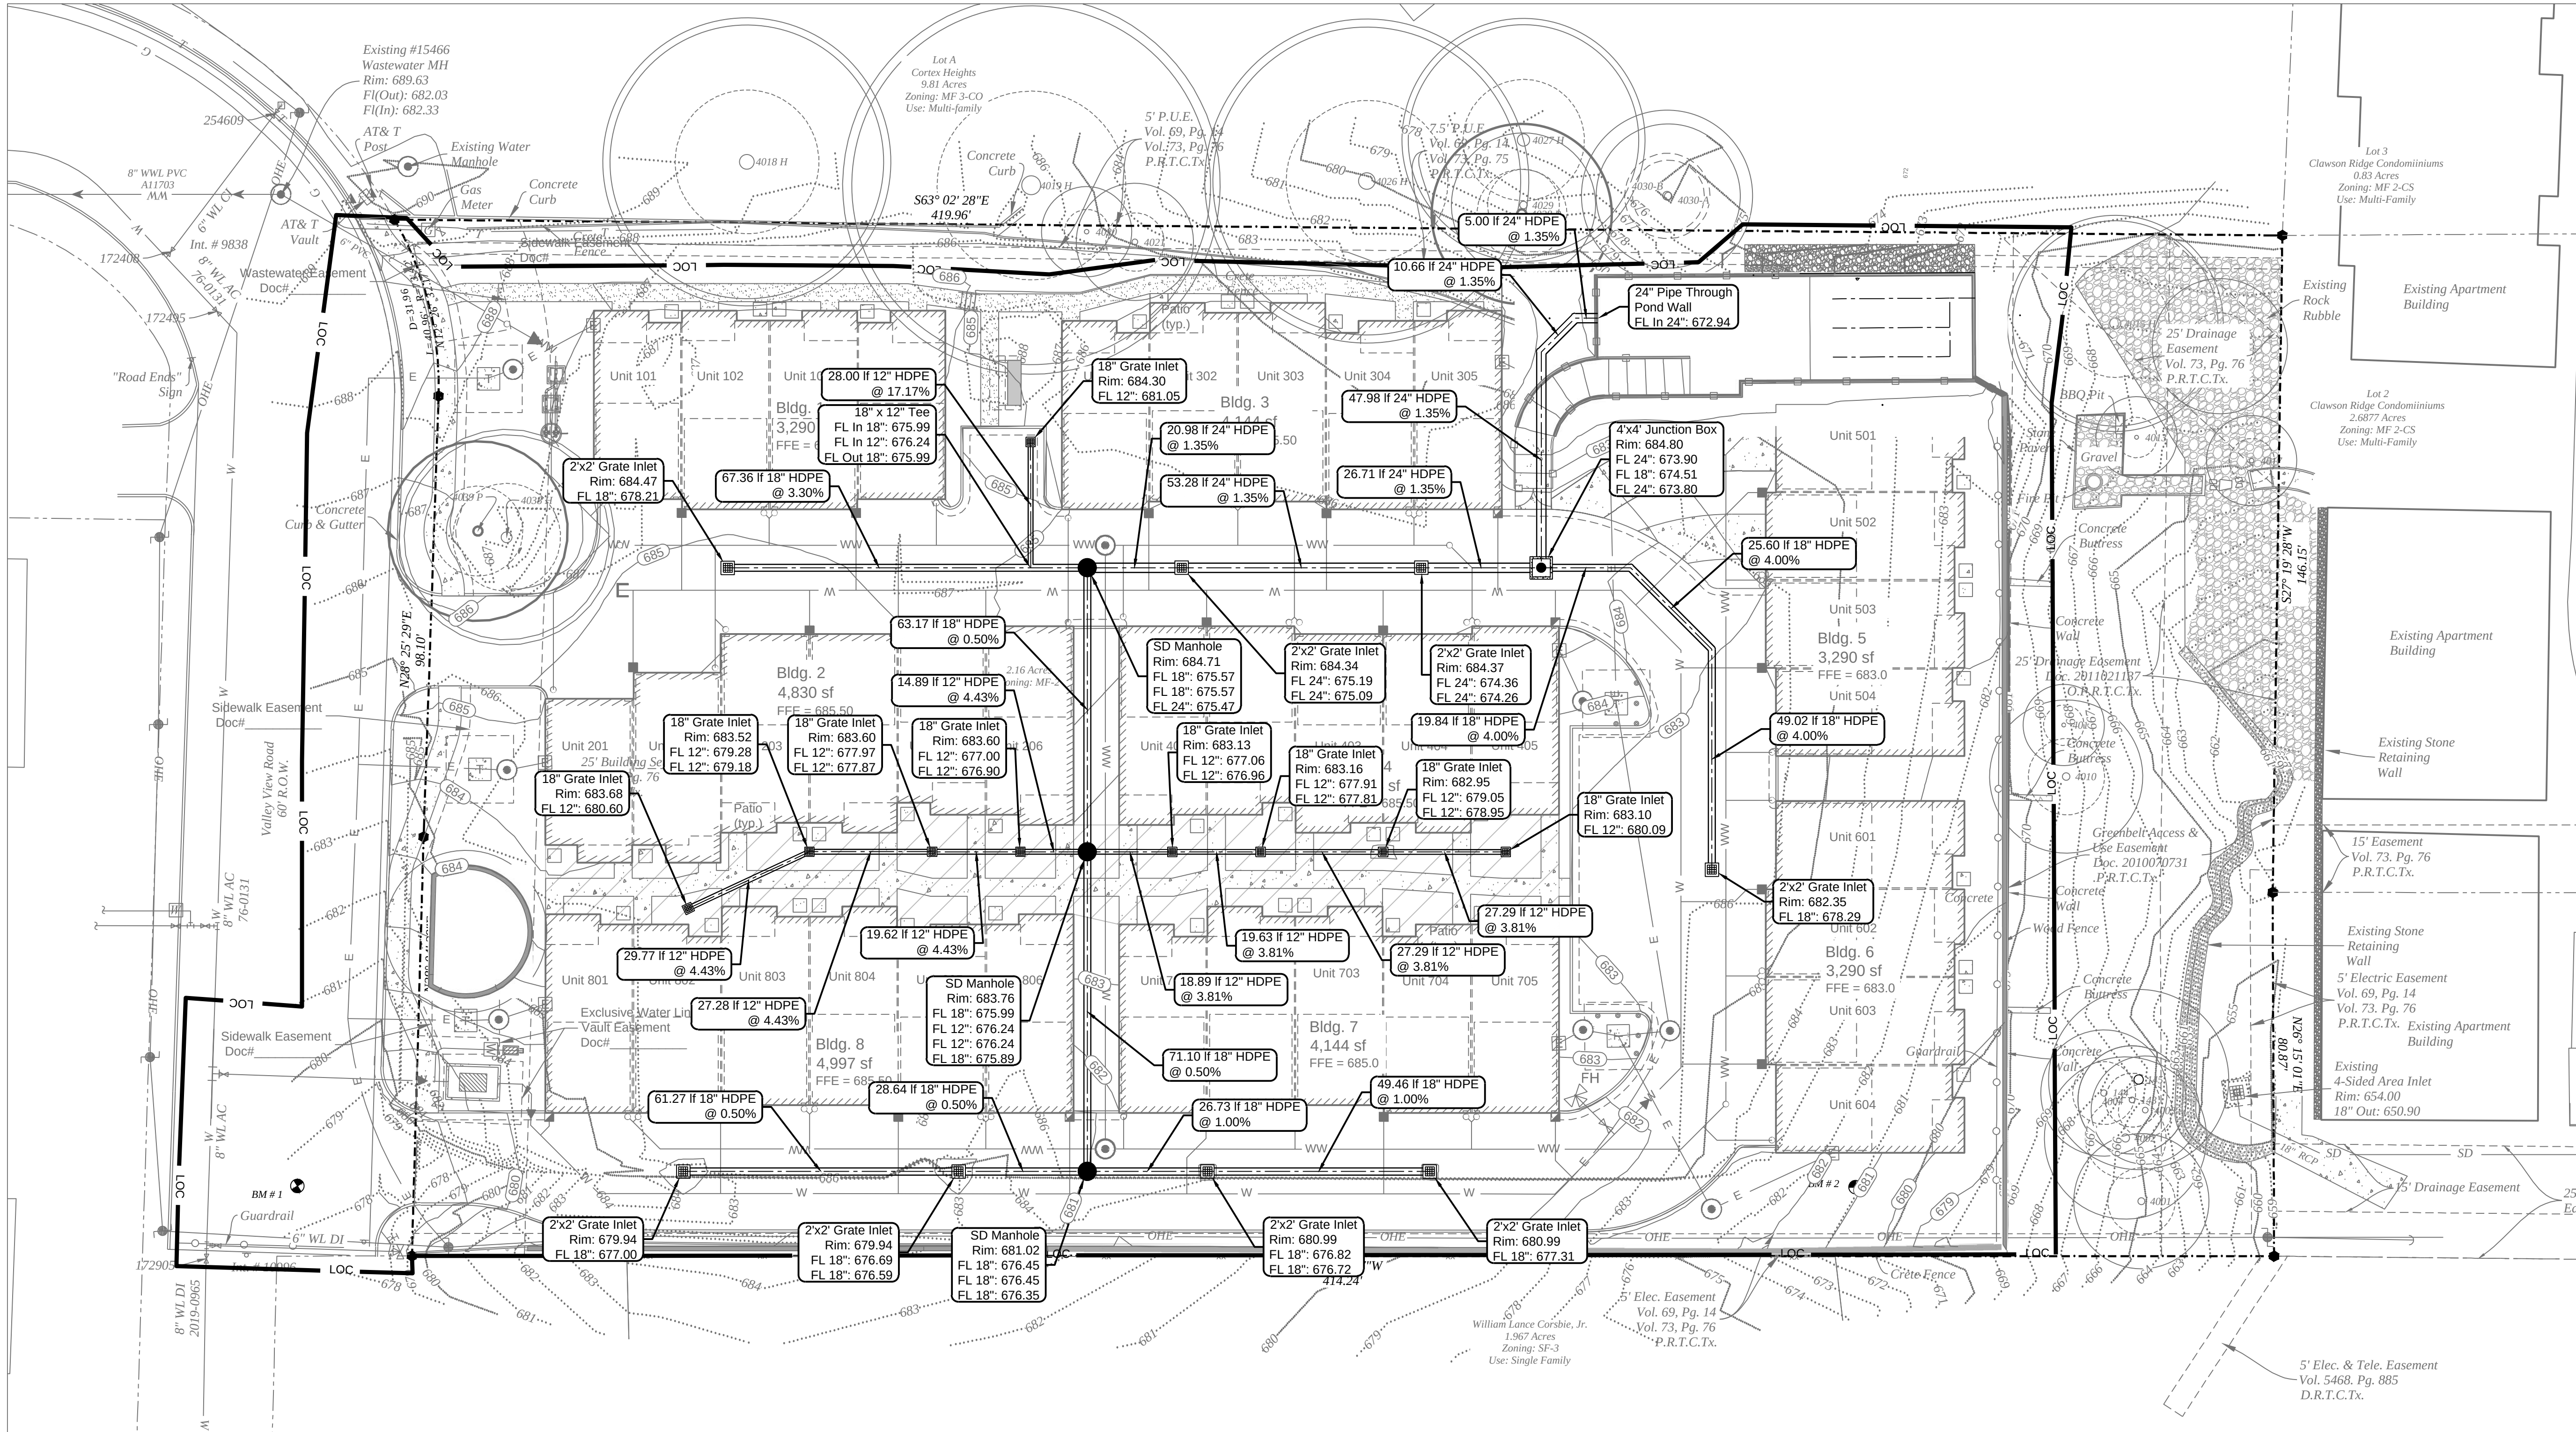

Legend

- Existing Contour
- Proposed Contour
- Proposed Spot Elevation
- Top of Curb
- Bottom of Curb
- Proposed Limits of Construction
- Proposed Storm Drain Line
- Level Landing (Not to exceed 2% in any Direction)
- ADA Ramp (Not to exceed 8.33%)

Drainage Notes

1. Upon completion of the proposed site improvements, and prior to the release of the Certificate of Occupancy by the Watershed Protection and Development Review Department, the Design Engineer shall certify in writing that the proposed detention and filtration facilities were constructed in conformance with the approved plans.

2. Contractor shall call One Call Center (472-2822) for utility locations prior to any work in City easements or street R.O.W.

Curb Note

Grading lines that indicate flows toward the curb shall be constructed as a catch curb. Grade lines that indicate flows away from curb shall be constructed as a spill curb.

Tree List

Refer to landscape plan sheet 32 for the tree list.


Benchmarks

B.M. #1 - Mag Nail Set in Asphalt
Elevation = 678.52' NAVD 88 (GEOID 18)

B.M. #2 - Mag Nail Set in Asphalt
Elevation = 681.08' NAVD 88 (GEOID 18)

Legal Description

Lot 1, Mecey Subdivision Volume 73, Page 76, Plat Records of Travis County, Texas.

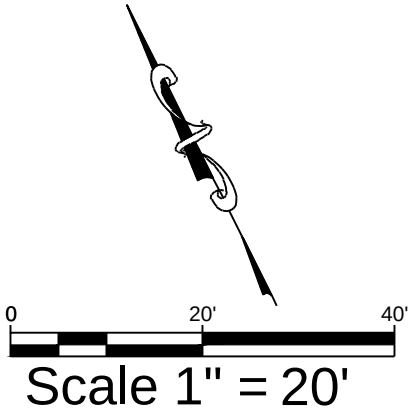

Release of this application does not constitute a verification of all data, information and calculations supplied by the applicant. The engineer of record is solely responsible for the completeness, accuracy and adequacy of his/her submittal, whether or not the application is reviewed for Code compliance by City engineers.

The location of all existing utilities shown on these plans has been based upon record information only and may not match locations as constructed. The contractor shall contact Texas 811 for assistance in determining existing utility locations prior to beginning construction. Contractor shall field verify locations of utility crossings prior to beginning construction.

Bleyl Engineering
Planning • Design • Management
7701 San Felipe Blvd., Suite 200, Austin TX 78729
Texas Firm Registration No. F-678
Tel. 512-454-2400
www.bleylengineering.com

Storm Sewer Plan

Valley View Townhomes
3759 Valley View Road
Austin, Texas 78704
Travis County

Professional Engineer
JASON K. RODGERS
87881
REGISTERED
2/27/26

Design: CS, JR
CAD: JW, CS | Review: JKR
Project No: RJ3 70496
Sheet: **12 of 39**
SP-2025-0126C