Figure 1.4.5.G.3 Silt Fence Placement for Perimeter Control

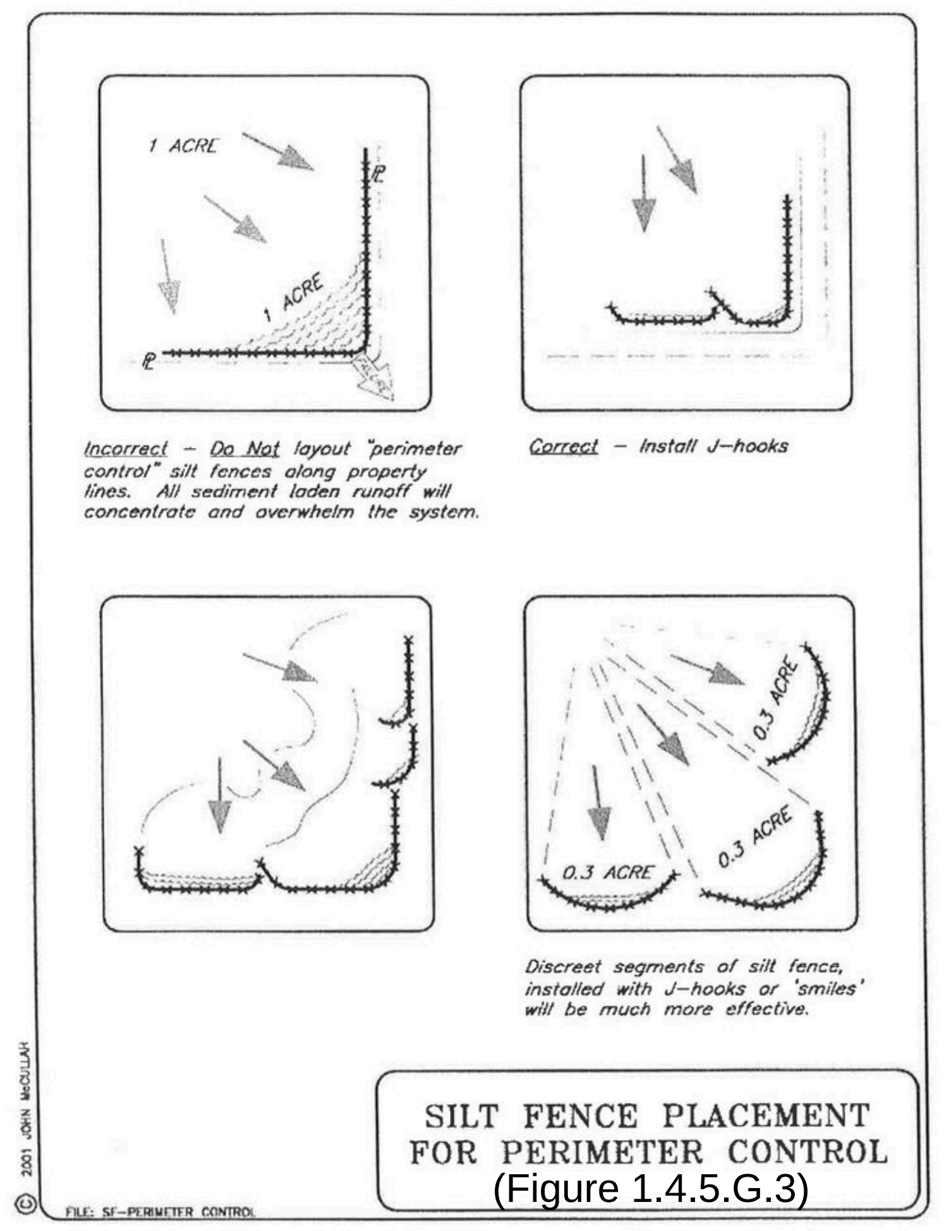
1 ACRE
1 ACRE
Incorrect – Do Not layout "perimeter control" silt fences along property lines. All sediment laden runoff will concentrate and overwhelm the system.
Correct – Install J–hooks
0.3 ACRE
0.3 ACRE
0.3 ACRE
Discreet segments of silt fence, installed with J–hooks or 'smiles' will be much more effective.
© 2001 JOHN McCULLAH
FILE: SF–PERIMETER CONTROL

SILT FENCE PLACEMENT FOR PERIMETER CONTROL
(Figure 1.4.5.G.3)

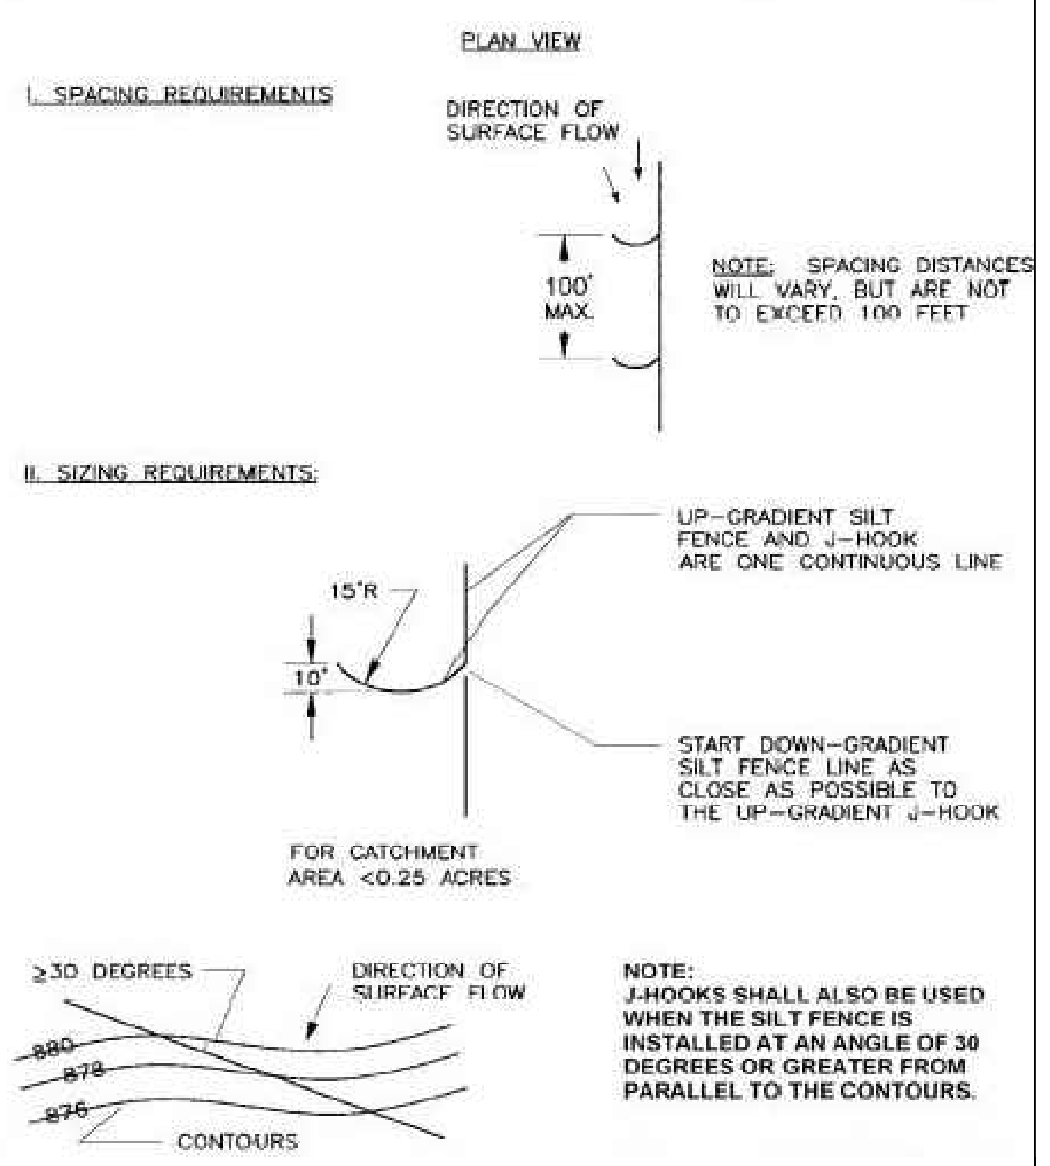
PLAN VIEW
I. SPACING REQUIREMENTS
DIRECTION OF SURFACE FLOW
100' MAX.
NOTE: SPACING DISTANCES WILL VARY, BUT ARE NOT TO EXCEED 100 FEET
II. SIZING REQUIREMENTS:
UP–GRADIENT SILT FENCE AND J–HOOK ARE ONE CONTINUOUS LINE
15'R
10'
START DOWN–GRADIENT SILT FENCE LINE AS CLOSE AS POSSIBLE TO THE UP–GRADIENT J–HOOK
FOR CATCHMENT AREA <0.25 ACRES
≥30 DEGREES
DIRECTION OF SURFACE FLOW
880
878
876
CONTOURS

NOTE:
J-HOOKS SHALL ALSO BE USED WHEN THE SILT FENCE IS INSTALLED AT AN ANGLE OF 30 DEGREES OR GREATER FROM PARALLEL TO THE CONTOURS.

Silt Fence J - Hook Detail
(Figure 1.4.5.G.4)

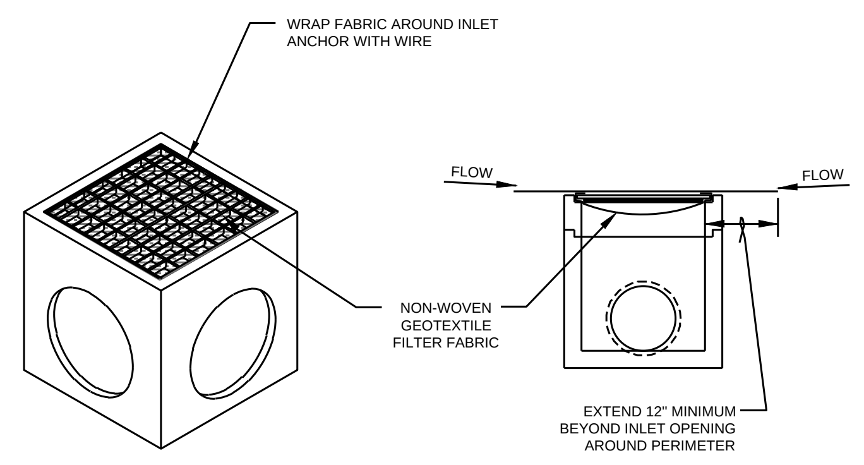
WRAP FABRIC AROUND INLET ANCHOR WITH WIRE
FLOW
FLOW
NON-WOVEN GEOTEXTILE FILTER FABRIC
EXTEND 12" MINIMUM BEYOND INLET OPENING AROUND PERIMETER

FILTER FABRIC SPECIFICATION TABLE

PROPERTY	TEST METHOD	ASTM REQUIREMENTS
FABRIC WEIGHT	D 3776	P3.0 OUNCES/SQUARE YARD
UV RADIATION STABILITY	D 4355	70% STRENGTH RETAINED MIN., AFTER 500 HOURS IN XENON ARC DEVICE
MULLEN BURST STRENGTH	D 3786	P120 POUND PER SQUARE INCH
WATER FLOW RATE	D 4491	P275 GALLONS/MINUTE/SQUARE FEET

Contact GeoSolutions at 512-445-0790 for filter fabric

NOTES
1. DAILY INSPECTION SHALL BE MADE BY THE CONTRACTOR AND SILT ACCUMULATION MUST BE REMOVED WHEN DEPTH REACHES 2". DO NOT ALLOW SILT TO ENTER STORM SYSTEM WHEN REMOVING INLET.
2. CONTRACTOR SHALL MONITOR THE PERFORMANCE OF INLET PROTECTION DURING EACH RAINFALL EVENT AND IMMEDIATELY CLEAN THE INLET PROTECTION IF EXCESSIVE PONDING OCCURS.
3. INLET PROTECTIONS SHALL BE REMOVED AS SOON AS THE SOURCE OF SEDIMENT IS STABILIZED.

THE ARCHITECT/ENGINEER ASSUMES RESPONSIBILITY FOR THE APPROPRIATE USE OF THIS DETAIL.

AREA INLET PROTECTION DETAIL

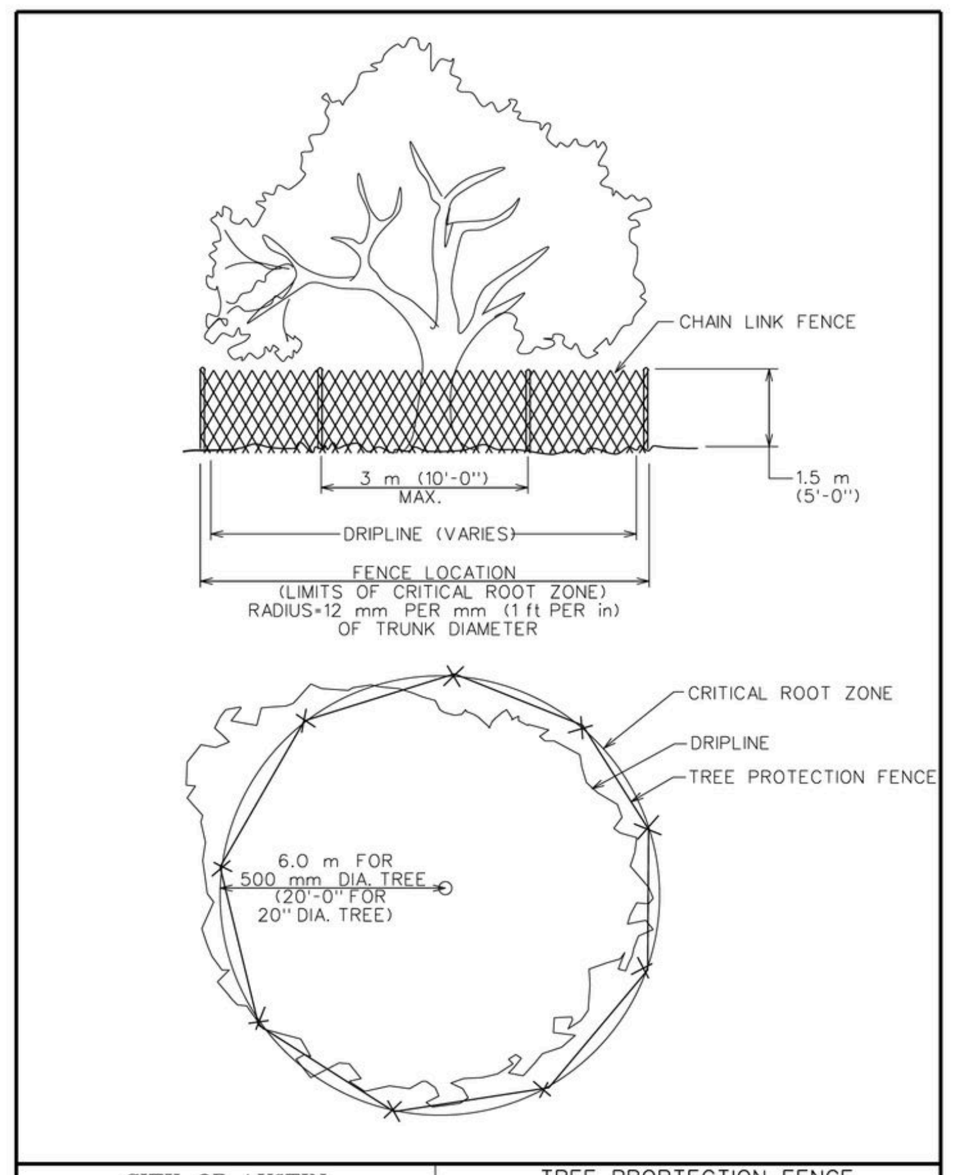
CHAIN LINK FENCE
3 m (10'-0") MAX.
1.5 m (5'-0")
DRIPLINE (VARIES)
FENCE LOCATION (LIMITS OF CRITICAL ROOT ZONE) RADIUS=12 mm PER mm (1 ft PER in) OF TRUNK DIAMETER
CRITICAL ROOT ZONE
DRIPLINE
TREE PROTECTION FENCE
6.0 m FOR 500 mm DIA. TREE (20'-0" FOR 20" DIA. TREE)

CITY OF AUSTIN WATERSHED PROTECTION DEPARTMENT	TREE PROPTECTION FENCE TYPE A - CHAIN LINK	
RECORD COPY SIGNED BY J. PATRICK MURPHY — 11/15/99 ADOPTED	THE ARCHITECT/ENGINEER ASSUMES RESPONSIBILITY FOR APPROPRIATE USE OF THIS STANDARD.	STANDARD NO. 610S-2

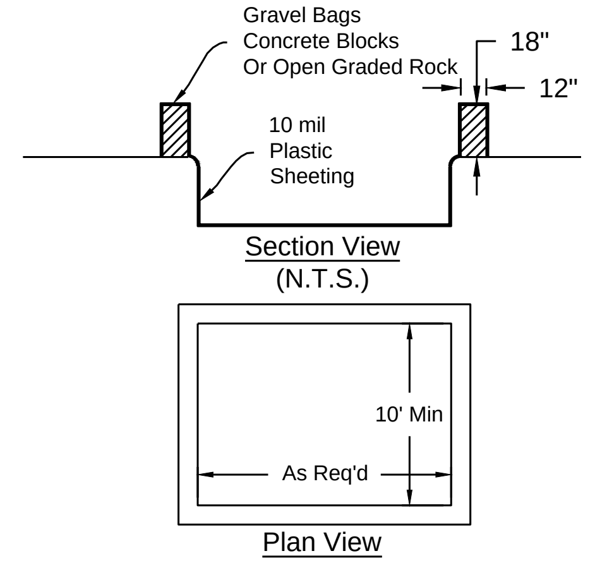

Alternative Self-Installed Construction Site Concrete Truck Washout

1. The excavation for the concrete truck washout shall be a minimum of 10' wide and of sufficient length and depth to accommodate 7 gallons of washout water and concrete per truck per day and/or 50 gallons of washout water and concrete per pump truck per day.
2. In the event that the self-installed concrete truck washout is constructed above ground, it shall be 10' wide and 10' long with the same requirements for containment as described in item 1.
3. The containment area shall be lined with 10 mil plastic sheeting, without holes or tears. Where there are seams, these shall be secured according to manufacturers directions.
4. The plastic sheeting shall be of sufficient size so that it will overlap the top of the containment area and be wrapped around the gravel bags, concrete blocks or open graded rock as least 2 times.
5. The gravel bags or concrete blocks shall be placed abutting each other to form a continuous berm around the outer perimeter of the containment area.
6. The berm consisting of gravel bags, concrete blocks or open graded rock shall be no less than 18" high and no less that 12" wide.
7. The containment area shall not exceed 50% of capacity at any one time.
8. Solids shall be removed from containment area and disposed of properly and any damage to the plastic sheeting shall be repaired or sheeting replaced before next use.

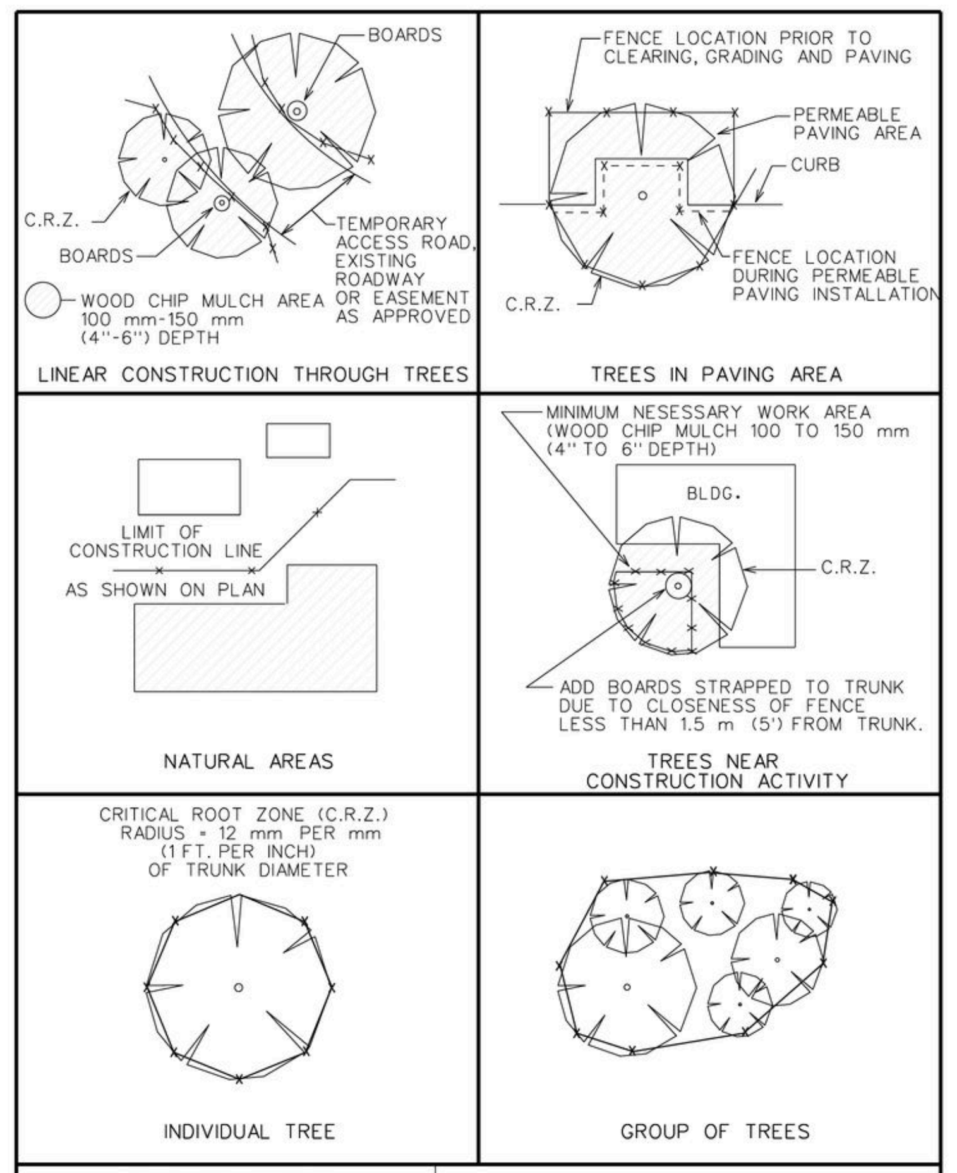
BOARDS
C.R.Z.
BOARDS
TEMPORARY ACCESS ROAD, EXISTING ROADWAY OR EASEMENT AS APPROVED
WOOD CHIP MULCH AREA 100 mm-150 mm (4"-6") DEPTH
LINEAR CONSTRUCTION THROUGH TREES
FENCE LOCATION PRIOR TO CLEARING, GRADING AND PAVING
PERMEABLE PAVING AREA
CURB
FENCE LOCATION DURING PERMEABLE PAVING INSTALLATION
C.R.Z.
TREES IN PAVING AREA
LIMIT OF CONSTRUCTION LINE AS SHOWN ON PLAN
NATURAL AREAS
MINIMUM NESESSARY WORK AREA (WOOD CHIP MULCH 100 TO 150 mm (4" TO 6" DEPTH)
BLDG.
C.R.Z.
ADD BOARDS STRAPPED TO TRUNK DUE TO CLOSENESS OF FENCE LESS THAN 1.5 m (5') FROM TRUNK.
TREES NEAR CONSTRUCTION ACTIVITY
CRITICAL ROOT ZONE (C.R.Z.) RADIUS = 12 mm PER mm (1 FT. PER INCH) OF TRUNK DIAMETER
INDIVIDUAL TREE
GROUP OF TREES

CITY OF AUSTIN WATERSHED PROTECTION DEPARTMENT	TREE PROTECTION FENCE LOCATIONS	
RECORD COPY SIGNED BY J. PATRICK MURPHY — 11/15/99 ADOPTED	THE ARCHITECT/ENGINEER ASSUMES RESPONSIBILITY FOR APPROPRIATE USE OF THIS STANDARD.	STANDARD NO. 610S-1

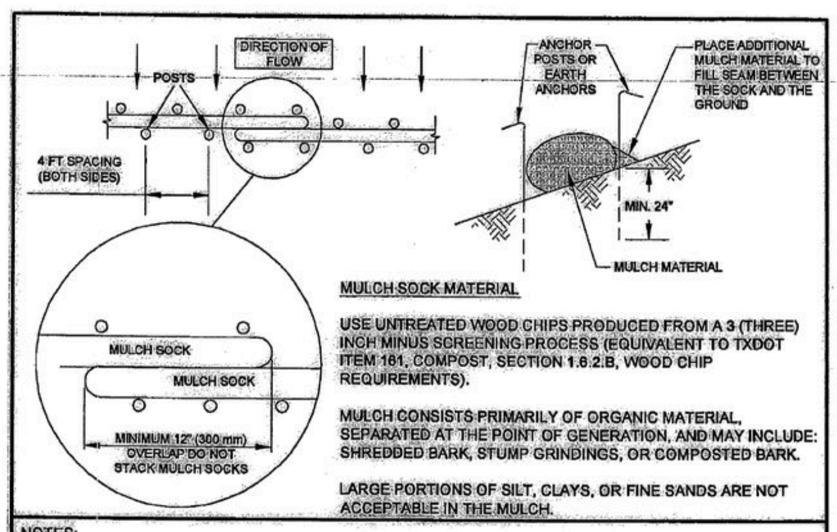
DIRECTION OF FLOW
POSTS
4 FT SPACING (BOTH SIDES)
ANCHOR POSTS OR EARTH ANCHORS
PLACE ADDITIONAL MULCH MATERIAL TO FILL SEAM BETWEEN THE SOCK AND THE GROUND
MIN. 24"
MULCH MATERIAL
MULCH SOCK
MULCH SOCK
MINIMUM 12" (300 mm) OVERLAP DO NOT STACK MULCH SOCKS

MULCH SOCK MATERIAL

USE UNTREATED WOOD CHIPS PRODUCED FROM A 3 (THREE) INCH MINUS SCREENING PROCESS (EQUIVALENT TO TXDOT ITEM 161, COMPOST, SECTION 1.6.2.B, WOOD CHIP REQUIREMENTS).

MULCH CONSISTS PRIMARILY OF ORGANIC MATERIAL, SEPARATED AT THE POINT OF GENERATION, AND MAY INCLUDE: SHREDDED BARK, STUMP GRINDINGS, OR COMPOSTED BARK.

LARGE PORTIONS OF SILT, CLAYS, OR FINE SANDS ARE NOT ACCEPTABLE IN THE MULCH.

NOTES:

1. STEEL OR WOOD POSTS WHICH SUPPORT THE MULCH SOCK SHALL BE INSTALLED ON A SLIGHT ANGLE TOWARD THE ANTICIPATED RUNOFF SOURCE. POST MUST BE EMBEDDED A MINIMUM OF 600mm (24 inches). IF WOOD POSTS CANNOT ACHIEVE 600mm (24 inches) DEPTH, USE STEEL POSTS. EARTH ANCHORS ARE ALSO ACCEPTABLE.
2. THE TOE OF THE MULCH SOCK SHALL BE PLACED SO THAT THE MULCH SOCK IS FLAT AND PERPENDICULAR TO THE LINE OF FLOW. IN ORDER TO PREVENT WATER FROM FLOWING BETWEEN THE JOINTS OF ADJACENT ENDS OFMULCH SOCKS, LAP THE ENDS OF ADJACENT MULCH SOCKS A MINIMUM OF 300mm (12 inches).
3. MULCH MATERIAL MUST BE FREE OF REFUSE, PHYSICAL CONTAMINANTS, AND MATERIAL TOXIC TO PLANT GROWTH; IT IS NOT ACCEPTABLE FOR THE MULCH MATERIAL TO CONTAIN GROUND CONSTRUCTION DEBRIS, BIOSOLIDS, OR MANURE.
4. SOCK MATERIAL WILL BE 100% BIODEGRADABLE, PHOTODEGRADABLE, OR RECYCLABLE SUCH AS BURLAP, TWINE, UV PHOTOBIODEGRADABLE PLASTIC, POLYESTER, OR ANY OTHER ACCEPTABLE MATERIAL.
5. MULCH SOCKS SHOULD BE USED AT THE BASE OF SLOPES NO STEEPER THAN 2:1 AND SHOULD NOT EXCEED THE MAXIMUM SPACING CRITERIA PROVIDED IN CITY OF AUSTIN ENVIRONMENTAL CRITERIA MANUAL TABLE 1.4.5.F.1 FOR A GIVEN SLOPE CATEGORY.
6. ACCUMULATED SILT SHALL BE REMOVED WHEN IT REACHES A DEPTH OF 150mm (6 inches). THE SILT SHALL BE DISPOSED OF ON AN APPROVED SITE AND IN SUCH A MANNER THAT WILL NOT CONTRIBUTE TO ADDITIONAL SILTATION.

CITY OF AUSTIN WATERSHED PROTECTION DEPARTMENT	MULCH SOCK	
Myron S. Rhyp P.E. 08/24/2010 ADOPTED	THE ARCHITECT/ENGINEER ASSUMES RESPONSIBILITY FOR APPROPRIATE USE OF THIS STANDARD.	STANDARD NO. 648S-1

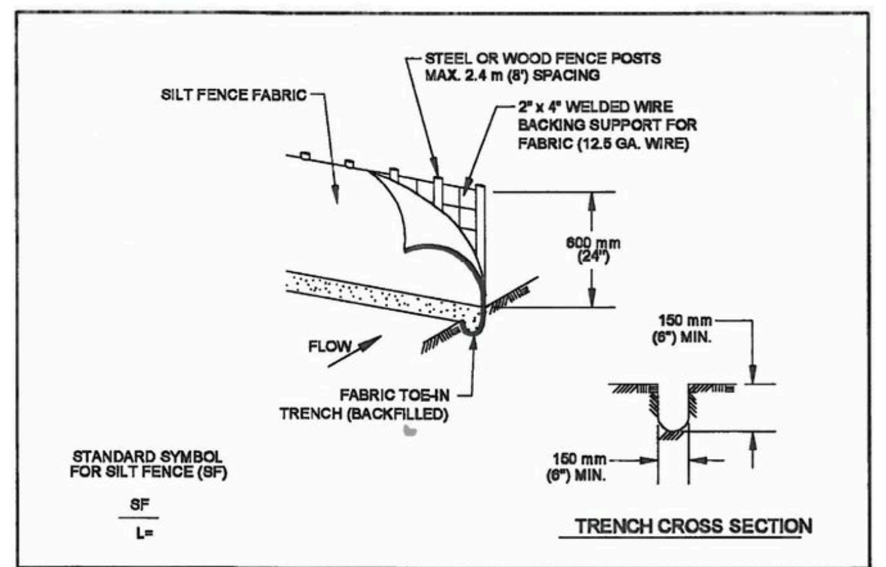
STEEL OR WOOD FENCE POSTS MAX. 2.4 m (8') SPACING
SILT FENCE FABRIC
2" x 4" WELDED WIRE BACKING SUPPORT FOR FABRIC (12.5 GA. WIRE)
600 mm (24")
150 mm (6") MIN.
FLOW
FABRIC TOE-IN TRENCH (BACKFILLED)
STANDARD SYMBOL FOR SILT FENCE (SF)
SF
L=
150 mm (6") MIN.
TRENCH CROSS SECTION

1. STEEL OR WOOD POSTS WHICH SUPPORT THE SILT FENCE SHALL BE INSTALLED ON A SLIGHT ANGLE TOWARD THE ANTICIPATED RUNOFF SOURCE. POST MUST BE EMBEDDED A MINIMUM OF 300 mm (12 INCHES). IF WOOD POSTS CANNOT ACHIEVE 300 mm (12 inches) DEPTH, USE STEEL POSTS.
2. THE TOE OF THE SILT FENCE SHALL BE TRENCHED IN WITH A SPADE OR MECHANICAL TRENCHER, SO THAT THE DOWNSLOPE FACE OF THE TRENCH IS FLAT AND PERPENDICULAR TO THE LINE OF FLOW.
3. THE TRENCH MUST BE A MINIMUM OF 150 mm (6 inches) DEEP AND 150 mm (6 inches) WIDE TO ALLOW FOR THE SILT FENCE FABRIC TO BE LAID IN THE GROUND AND BACKFILLED WITH COMPACTED MATERIAL.
4. SILT FENCE FABRIC SHOULD BE SECURELY FASTENED TO EACH STEEL OR WOOD SUPPORT POST OR TO WOVEN WIRE , WHICH IS IN TURN ATTACHED TO THE STEEL OR WOOD FENCE POST.
5. INSPECTION SHALL BE MADE WEEKLY OR AFTER EACH RAINFALL EVENT AND REPAIR OR REPLACEMENT SHALL BE MADE PROMPTY AS NEEDED.
6. SILT FENCE SHALL BE REMOVED WHEN THE SITE IS COMPLETELY STABILIZED SO AS NOT TO BLOCK OR IMPEDE STORM FLOW OR DRAINAGE.
7. ACCUMULATED SILT SHALL BE REMOVED WHEN IT REACHES A DEPTH OF 150 mm (6 inches). THE SILT SHALL BE DISPOSED OF ON AN APPROVED SITE AND IN SUCH A MANNER THAT WILL NOT CONTRIBUTE TO ADDITIONAL SILTATION.

CITY OF AUSTIN WATERSHED PROTECTION DEPARTMENT	SILT FENCE	
9/1/2011 ADOPTED	THE ARCHITECT/ENGINEER ASSUMES RESPONSIBILITY FOR APPROPRIATE USE OF THIS STANDARD.	STANDARD NO. 642S-1

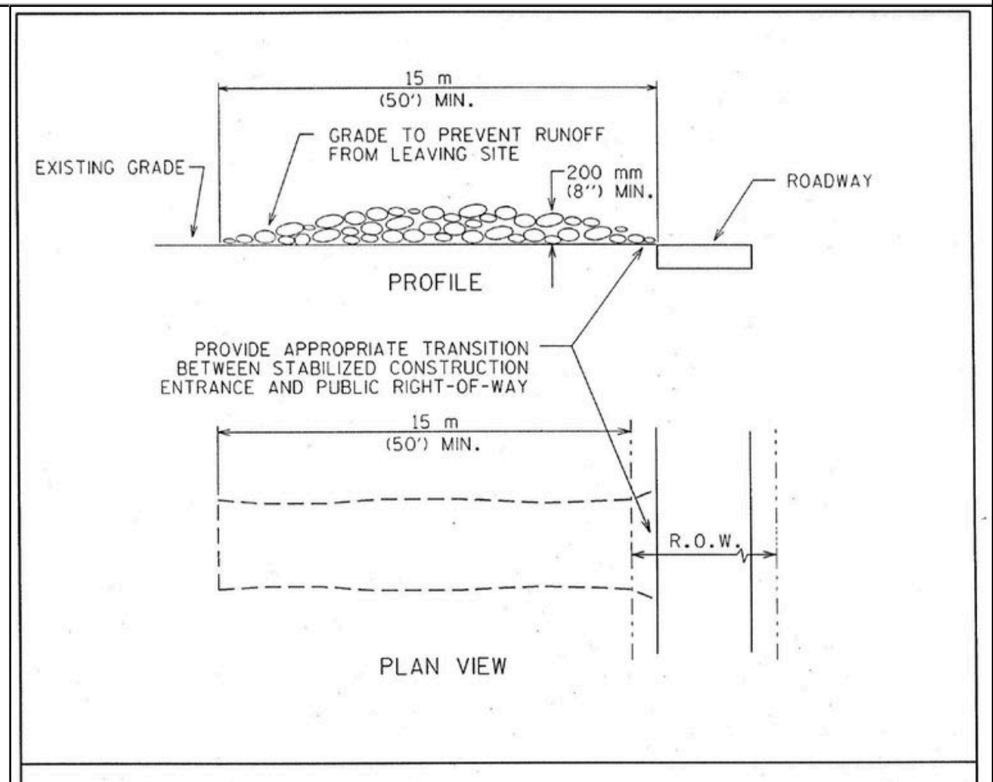
15 m (50') MIN.
GRADE TO PREVENT RUNOFF FROM LEAVING SITE
EXISTING GRADE
200 mm (8") MIN.
ROADWAY
PROFILE
PROVIDE APPROPRIATE TRANSITION BETWEEN STABILIZED CONSTRUCTION ENTRANCE AND PUBLIC RIGHT-OF-WAY
15 m (50') MIN.
R.O.W.
PLAN VIEW

NOTES:
1. STONE SIZE: 75-125 mm (3-5") OPEN GRADED ROCK.
2. LENGTH: AS EFFECTIVE BUT NOT LESS THAN 15 m (50').
3. THICKNESS: NOT LESS THAN 200 mm (8").
4. WIDTH: NOT LESS THAN FULL WIDTH OF ALL POINTS OF INGRESS/EGRESS.
5. WASHING: WHEN NECESSARY, VEHICLE WHEELS SHALL BE CLEANED TO REMOVE SEDIMENT PRIOR TO ENTRANCE ONTO PUBLIC ROADWAY. WHEN WASHING IS REQUIRED, IT SHALL BE DONE ON AN AREA STABILIZED WITH CRUSHED STONE AND DRAINS INTO AN APPROVED TRAP OR SEDIMENT BASIN. ALL SEDIMENT SHALL BE PREVENTED FROM ENTERING ANY STORM DRAIN, DITCH OR WATERCOURSE USING APPROVED METHODS.
6. MAINTENANCE: THE ENTRANCE SHALL BE MAINTAINED IN A CONDITION THAT WILL PREVENT TRACKING OR FLOWING OF SEDIMENT ONTO PUBLIC ROADWAY. THIS MAY REQUIRE PERIODIC TOP DRESSING WITH ADDITIONAL STONE AS CONDITIONS DEMAND, AS WELL AS REPAIR AND CLEAN OUT OF ANY MEASURE DEVICES USED TO TRAP SEDIMENT. ALL SEDIMENTS THAT IS SPILLED, DROPPED, WASHED OR TRACKED ONTO PUBLIC ROADWAY MUST BE REMOVED IMMEDIATELY.
7. DRAINAGE: ENTRANCE MUST BE PROPERLY GRADED OR INCORPORATE A DRAINAGE SWALE TO PREVENT RUNOFF FROM LEAVING THE CONSTRUCTION SITE.

CITY OF AUSTIN WATERSHED PROTECTION DEPARTMENT	STABILIZED CONSTRUCTION ENTRANCE	
Leon Barba 5/23/00 ADOPTED	THE ARCHITECT/ENGINEER ASSUMES RESPONSIBILITY FOR APPROPRIATE USE OF THIS STANDARD.	STANDARD NO. 641S-1

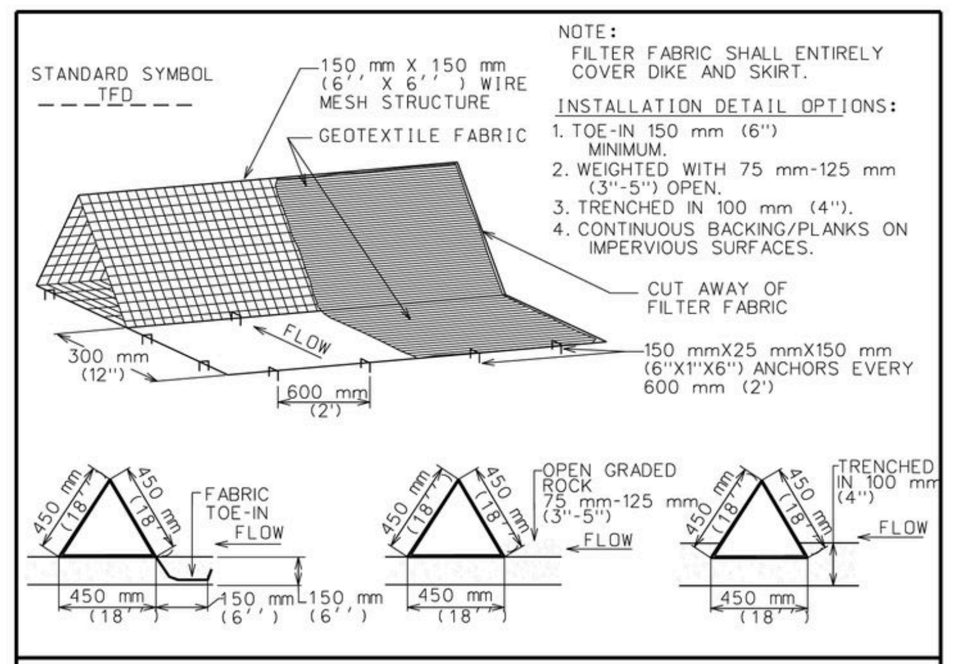

NOTE:
FILTER FABRIC SHALL ENTIRELY COVER DIKE AND SKIRT.

INSTALLATION DETAIL OPTIONS:
1. TOE-IN 150 mm (6") MINIMUM.
2. WEIGHTED WITH 75 mm-125 mm (3"-5") OPEN.
3. TRENCHED IN 100 mm (4").
4. CONTINUOUS BACKING/PLANKS ON IMPERVIOUS SURFACES.

GENERAL NOTES
1. DIKES SHALL BE PLACED IN A ROW WITH ENDS TIGHTLY ABUTTING THE ADJACENT DIKE.
2. THE FABRIC COVER AND SKIRT SHALL BE A CONTINUOUS WRAPPING OF GEOTEXTILE. THE SKIRT SHALL BE A CONTINUOUS EXTENSION OF THE FABRIC ON THE UPSTREAM FACE.
3. THE SKIRT SHALL BE WEIGHTED WITH A CONTINUOUS LAYER OF 75-125 mm (3-5") OPEN GRADED ROCK OR TOED-IN 150 mm (6") WITH MECHANICALLY COMPACTED MATERIAL. OTHERWISE, THE ENTIRE STRUCTURE SHALL BE TRENCHED IN 100 mm (4").
4. DIKES AND SKIRT SHALL BE SECURELY ANCHORED IN PLACE USING 150 mm (6") WIRE STAPLES ON 600 mm (2') CENTERS ON BOTH EDGES AND SKIRT, OR STAKE USING 10M (3/8") DIAMETER RE-BAR WITH TEE ENDS.
5. FILTER MATERIAL SHALL BE LAPPED OVER ENDS 150 mm (6") TO COVER DIKE TO DIKE JOINTS. JOINTS SHALL BE FASTENED WITH GALVANIZED SHOAT RINGS.
6. THE DIKE STRUCTURE SHALL BE MW40-150 mmX150 mm (6 GA. 6"X6") WIRE MESH, 450 mm (18") ON A SIDE.
7. INSPECTION SHALL BE MADE WEEKLY OR AFTER EACH RAINFALL EVENT AND REPAIR OR REPLACEMENT SHALL BE MADE PROMPTLY AS NEEDED BY THE CONTRACTOR.
8. ACCUMULATED SILT SHALL BE REMOVED WHEN IT REACHES A DEPTH OF 150 mm (6") AND DISPOSED OF IN A MANNER WHICH WILL NOT CAUSE ADDITIONAL SILTATION.
9. AFTER THE DEVELOPMENT SITE IS COMPLETLY STABILIZED, THE DIKES AND ANY REMAINING SILT SHALL BE REMOVED. SILT SHALL BE DISPOSED OF AS INDICATED IN GENERAL NOTE 8 ABOVE.

CITY OF AUSTIN WATERSHED PROTECTION DEPARTMENT	TRIANGULAR SEDIMENT FILTER DIKE	
RECORD COPY SIGNED BY J. PATRICK MURPHY — 3/27/00 ADOPTED	THE ARCHITECT/ENGINEER ASSUMES RESPONSIBILITY FOR APPROPRIATE USE OF THIS STANDARD.	STANDARD NO. 628S

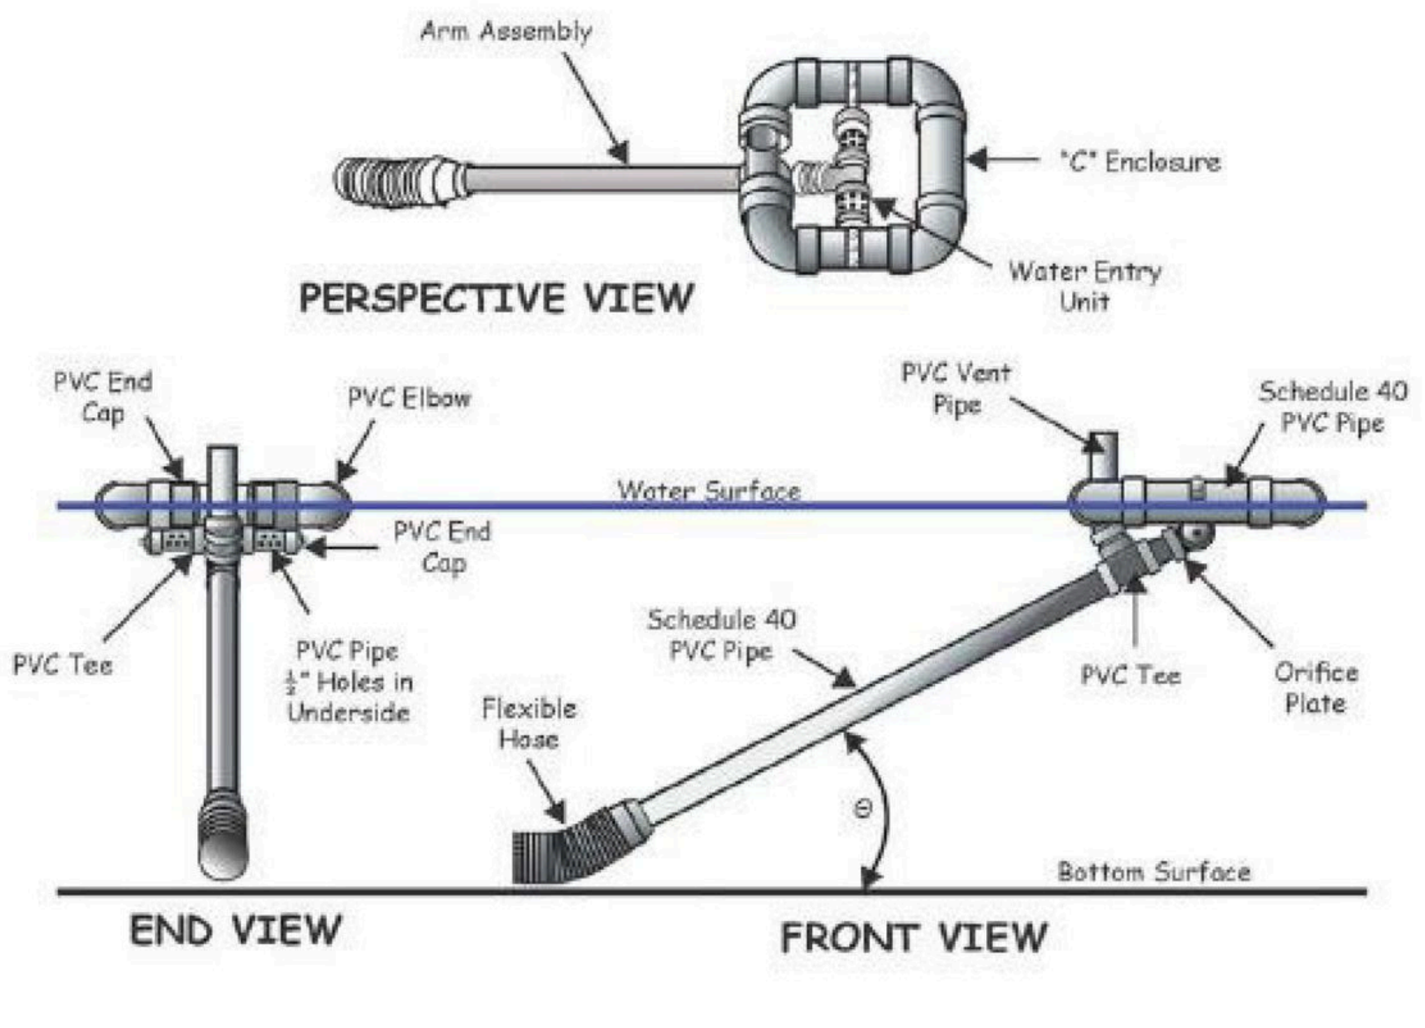

Figure 6.64a Schematic of a skimmer, from Pennsylvania Erosion and Sediment Pollution Control Manual, March, 2000.

Dewatering Skimmer
(Figure 1.4.5.K.1)

Release of this application does not constitute a verification of all data, information and calculations supplied by the applicant. The engineer of record is solely responsible for the completeness, accuracy and adequacy of his/her submittal, whether or not the application is reviewed for Code compliance by City engineers.

The location of all existing utilities shown on these plans has been based upon record information only and may not match locations as constructed. The contractor shall contact Texas 811 for assistance in determining existing utility locations prior to beginning construction. Contractor shall field verify locations of utility crossings prior to beginning construction.

Revision	Date	By	App	Comment

Bleyl Engineering
Planning • Design • Management
7701 San Felipe Blvd., Suite 200, Austin TX 78729
Texas Firm Registration No. F-678
Tel. 512-454-2400
www.bleylengineering.com
Austin Bryan Conroe Houston

Erosion Control Details

Valley View Townhomes
3759 Valley View Road
Austin, Texas 78704
Travis County

JASON K. RODGERS
87881
2/27/26

Design: CS, JR
CAD: JW, CS Review: JKR
Project No: RJ3 70496
Sheet: 7 of 39
SP-2025-0126C

ORIGINAL LAYOUT SIZE - 24X36

@2026 H:\JOBFILES\RJ3 (RJ3 BUILDING GROUP)\RJ3 70496 (VALLEY VIEW TOWNHOMES SP)\04 CAD\PLOT SHEETS\EROSION NOTES.DWG 2/27/2026 10:08 AM Chris Shaleesh