


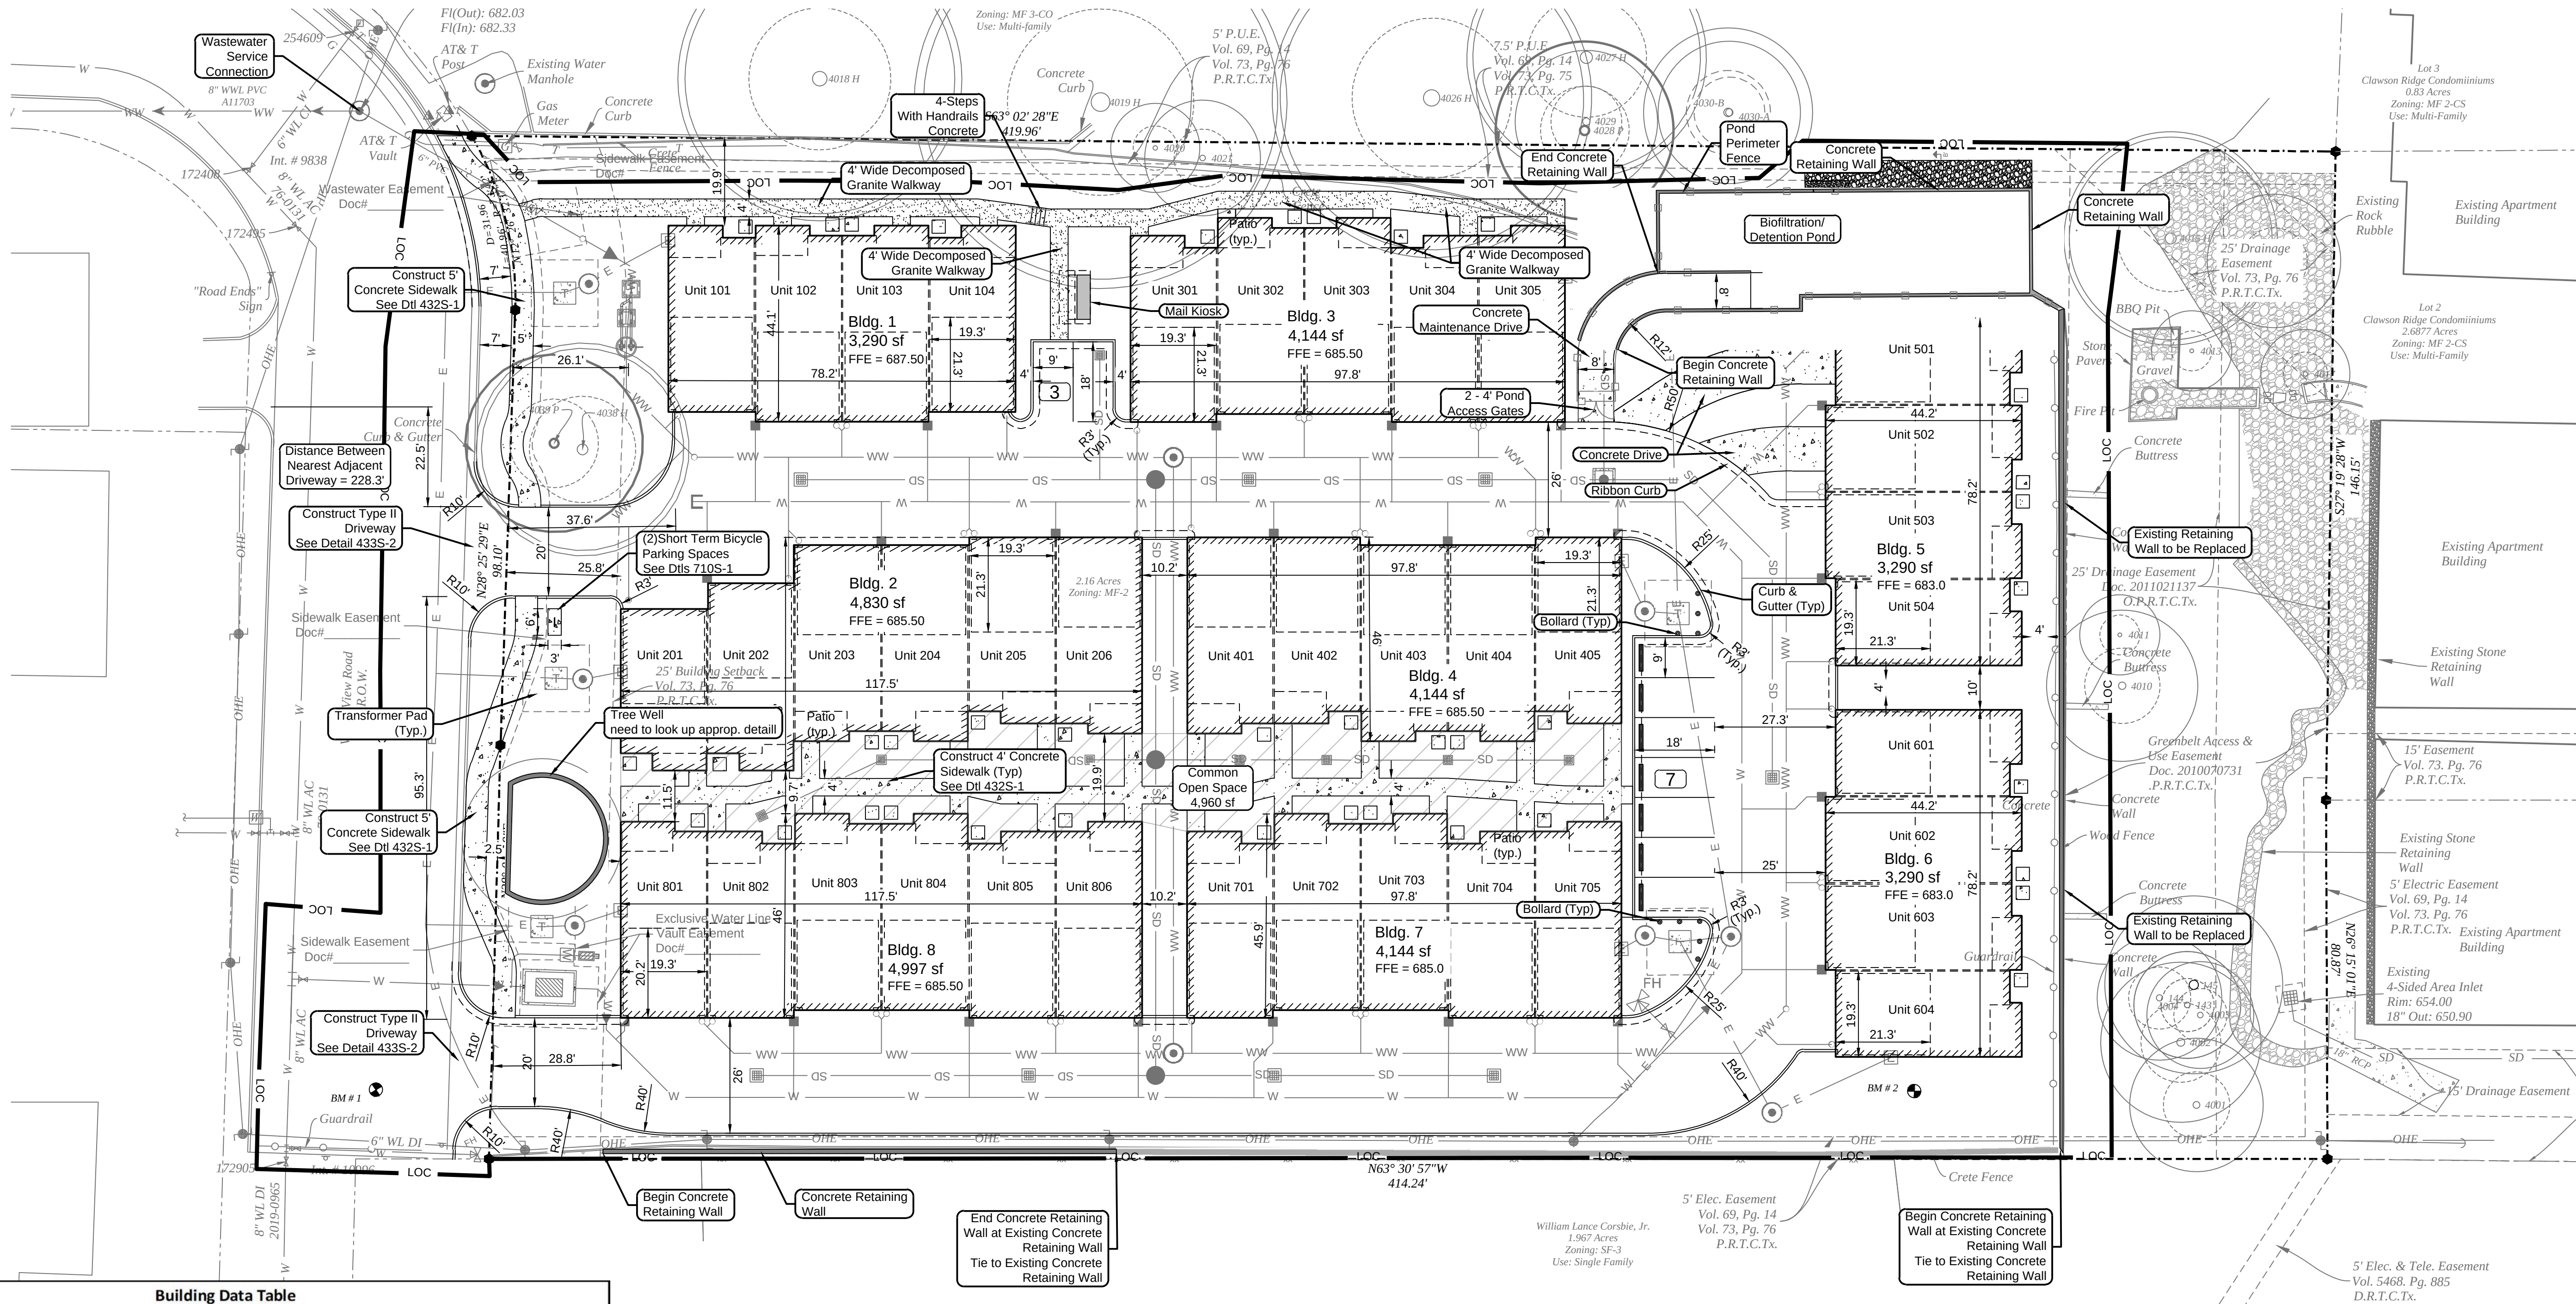

| Building # | Building Type | Gross Floor Area (sf) | Building Coverage (sf) | Bedroom Type                           | Units |
|------------|---------------|-----------------------|------------------------|----------------------------------------|-------|
| 1          | 4 Plex        | 8,550                 | 3,290                  | Two Bedroom                            | 16    |
| 2          | 6 Plex        | 13,004                | 4,997                  | Three Bedroom                          | 23    |
| 3          | 5 Plex        | 10,776                | 4,144                  | Total Units                            | 39    |
| 4          | 5 Plex        | 10,776                | 4,144                  | Maximum Number of Building Stories = 3 |       |
| 5          | 4 Plex        | 8,550                 | 3,290                  |                                        |       |
| 6          | 4 Plex        | 8,550                 | 3,290                  |                                        |       |
| 7          | 5 Plex        | 10,776                | 4,144                  |                                        |       |
| 8          | 6 Plex        | 13,004                | 4,997                  | Foundation = Slab on grade             |       |

| Site Area Calculation (MF-2)     |            |           |            |
|----------------------------------|------------|-----------|------------|
| Unit Type                        | Efficiency | 1 Bedroom | 2+ Bedroom |
| Number of Units                  | 0          | 0         | 39         |
| Required Site Area Per Unit (sf) | 1,600      | 2,000     | 2,400      |
| Site Area Required (sf)          | 0          | 0         | 93,600     |
| Total Site Area Required (sf)    |            | 93,600    |            |
| Total Site Area Provided (sf)    |            | 94,192    |            |

| Building # | Building Type | Average (MSL) | Building Height (FT) | Avg. Building Height (MSL) | Height Allowed (FT) | Height Allowed (MSL) |
|------------|---------------|---------------|----------------------|----------------------------|---------------------|----------------------|
| 1          | 4 Plex        | 686.25        | 35' - 10.75"         | 722.15                     | 40'                 | 726.25               |
| 2          | 6 Plex        | 684.50        | 33' - 4.75"          | 717.90                     | 40'                 | 724.50               |
| 3          | 5 Plex        | 685.00        | 36' - 1"             | 721.08                     | 40'                 | 725.00               |
| 4          | 5 Plex        | 684.25        | 33' - 4.75"          | 717.65                     | 40'                 | 724.25               |
| 5          | 4 Plex        | 682.17        | 35' - 10.75"         | 718.07                     | 40'                 | 722.17               |
| 6          | 4 Plex        | 681.75        | 35' - 10.75"         | 717.65                     | 40'                 | 721.75               |
| 7          | 5 Plex        | 682.50        | 33' - 4.75"          | 715.90                     | 40'                 | 722.50               |
| 8          | 6 Plex        | 682.25        | 33' - 4.75"          | 715.65                     | 40'                 | 722.25               |

| Zoning:                       | MF-2/Multi-Family Low Density |       |     |
|-------------------------------|-------------------------------|-------|-----|
| Use: Multi-Family Residential | s.f.                          | acres | %   |
| Site Area:                    | 94,192                        | 2.162 |     |
| Allowable Impervious Cover:   | 56,515                        | 1.297 | 60% |
| Existing Impervious Cover:    | 61,350                        | 1.408 | 65% |
| Impervious Cover Removed:     | 61,350                        | 1.408 | 65% |
| Total Impervious Cover:       | 55,502                        | 1.274 | 59% |
| Allowable Building Coverage:  | 47,096                        | 1.081 | 50% |
| Proposed Building Coverage:   | 32,296                        | 0.741 | 34% |
| Gross Floor Area:             | 83,986                        | 1.928 |     |
| Building Slab Construction    | Slab On Grade                 |       |     |
| Common Open Space Required    | 4709.62                       |       |     |
| Common Open Space provided    | 4710                          |       |     |

## Site Plan Release Notes

- a. All improvements shall be made in accordance with the released site plan. Any additional improvements will require site plan amendment and approval of the Development Services Department.
- b. Approval of this Site Plan does not include Building and Fire Code approval nor building permit approval.
- c. All signs must comply with requirements of the Land Development Code ([Chapter 25-10](#)).
- d. Additional electric easements may be required at a later date.
- e. Water and wastewater service will be provided by the City of Austin (or identify the service provider if other than the City of Austin).
- f. All existing structures shown to be removed will require a demolition permit from the City of Austin Development Services Department.
- g. No certificate of occupancy may be issued for the proposed residential condominium project until the owner or owners of the property have complied with Chapter 81 and 82 of the Property Code of the State of Texas or any other statutes enacted by the State concerning condominiums.
- h. For driveway construction: The owner is responsible for all costs for relocation of, or damage to utilities.
- i. For construction within the right-of-way, a ROW excavation permit is required.

### Lighting Note

All exterior lighting will be full cut-off and fully shielded in compliance with Subchapter E 2.5. All site lighting to be located on the building will be in compliance with Subchapter E 2.5, and will be reviewed during building plan review. Any change or substitution of lamps/light fixtures shall be submitted to the Director for approval in accordance with Section 2.5.2.E. See Figure 34.

## Trash Collection Notes

- Trash containers shall not be left at curb side unattended. Signs must be posted on the building or at a location that is publicly visible indicating that trash containers may not be left at curbside. The sign shall indicate the City of Austin's Code enforcement phone number for the public to report violations.
- A restrictive covenant may be required for enforcement purposes.

*Reference: TCM, 9.4.2*

## Accessibility Notes

1. Approval of these plans by the City of Austin indicates compliance with applicable City regulations only. Compliance with accessibility standards such as the 2010 Standards for Accessible Design or the 2012 Texas Accessibility Standards was not verified. The applicant is responsible for compliance with all applicable accessibility standards.
2. Accessible parking spaces must be located on a surface with a slope not exceeding 1:50.
3. Accessible routes must have a cross-slope no greater than 1:50.
4. Slopes on accessible routes may not exceed 1:20 unless designed as a ramp.
5. The maximum slope of a ramp in new construction is 1:12. The maximum rise for any ramp is 20in. The maximum horizontal projection is 30 feet for a ramp with a slope between 1:12 and 1:15, and 40 feet for a ramp with a slope between 1:16 and 1:20.

## Benchmarks

B.M. #1 - Mag Nail Set in Asphalt  
Elevation = 678.52' NAVD 88 (GEOID 18)

B.M. #2 - Mag Nail Set in Asphalt  
Elevation = 681.08' NAVD 88 (GEOID 18)

**Legal Description**  
Lot 1, Mecey Subdivision Volume 73, Page 76, Plat Records of Travis County, Texas.

|                                    | <u>Parking Data</u>   |
|------------------------------------|-----------------------|
| Land Use                           | Residential           |
| Parking Spaces Provided            | 10 Surface/ 78 Garage |
| Compact Spaces Provided            | 0                     |
| ADA Spaces Required                | X                     |
| ADA Spaces Provided                | X                     |
| Total Bicycle Spaces Required      | 5                     |
| Long Term Bicycle Spaces Required  | 3                     |
| Long Term Bicycle Spaces Provided  | 39 (1 per Garage)     |
| Short Term Bicycle Spaces Required | 2                     |
| Short Term Bicycle Spaces Provided | 2                     |

### Fence Note

Post holes that are to be installed near a trees Critical Root Zone (CRZ) will be dug by hand. No machinery is allowed in the CRZ and any work done in this area shall be done by hand. Add a 3-inch layer of hardwood mulch in the CRZ prior to commencing construction activities.

The location of all existing utilities shown on these plans has been based upon record information only and may not match locations as constructed. The contractor shall contact Texas 811 for assistance in determining existing utility locations prior to beginning construction. Contractor shall field verify locations of utility crossings prior to beginning construction.

